




MIDEA FURNITURE DETAIL

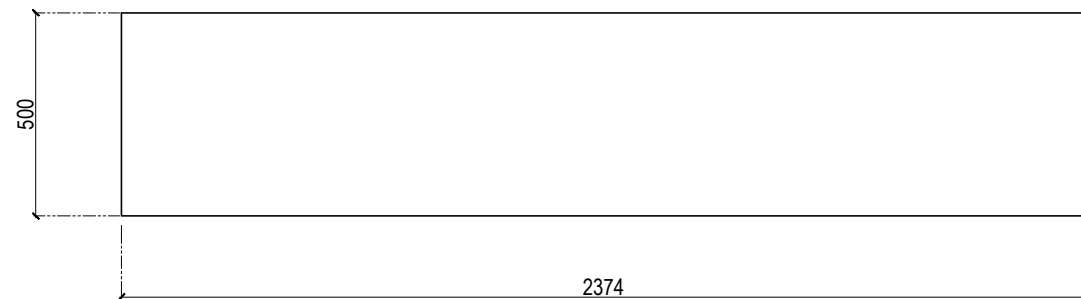


1 PLAN
WORKSTATION AREA STORAGE

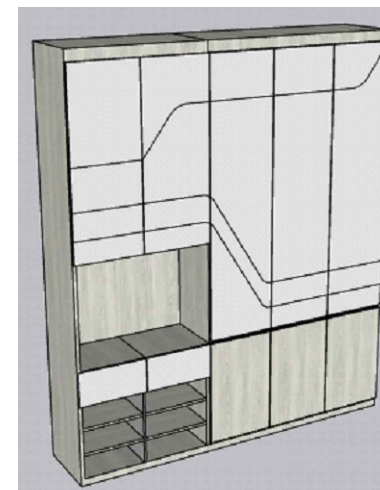

3 REFERENCE IMAGE
WORKSTATION AREA STORAGE

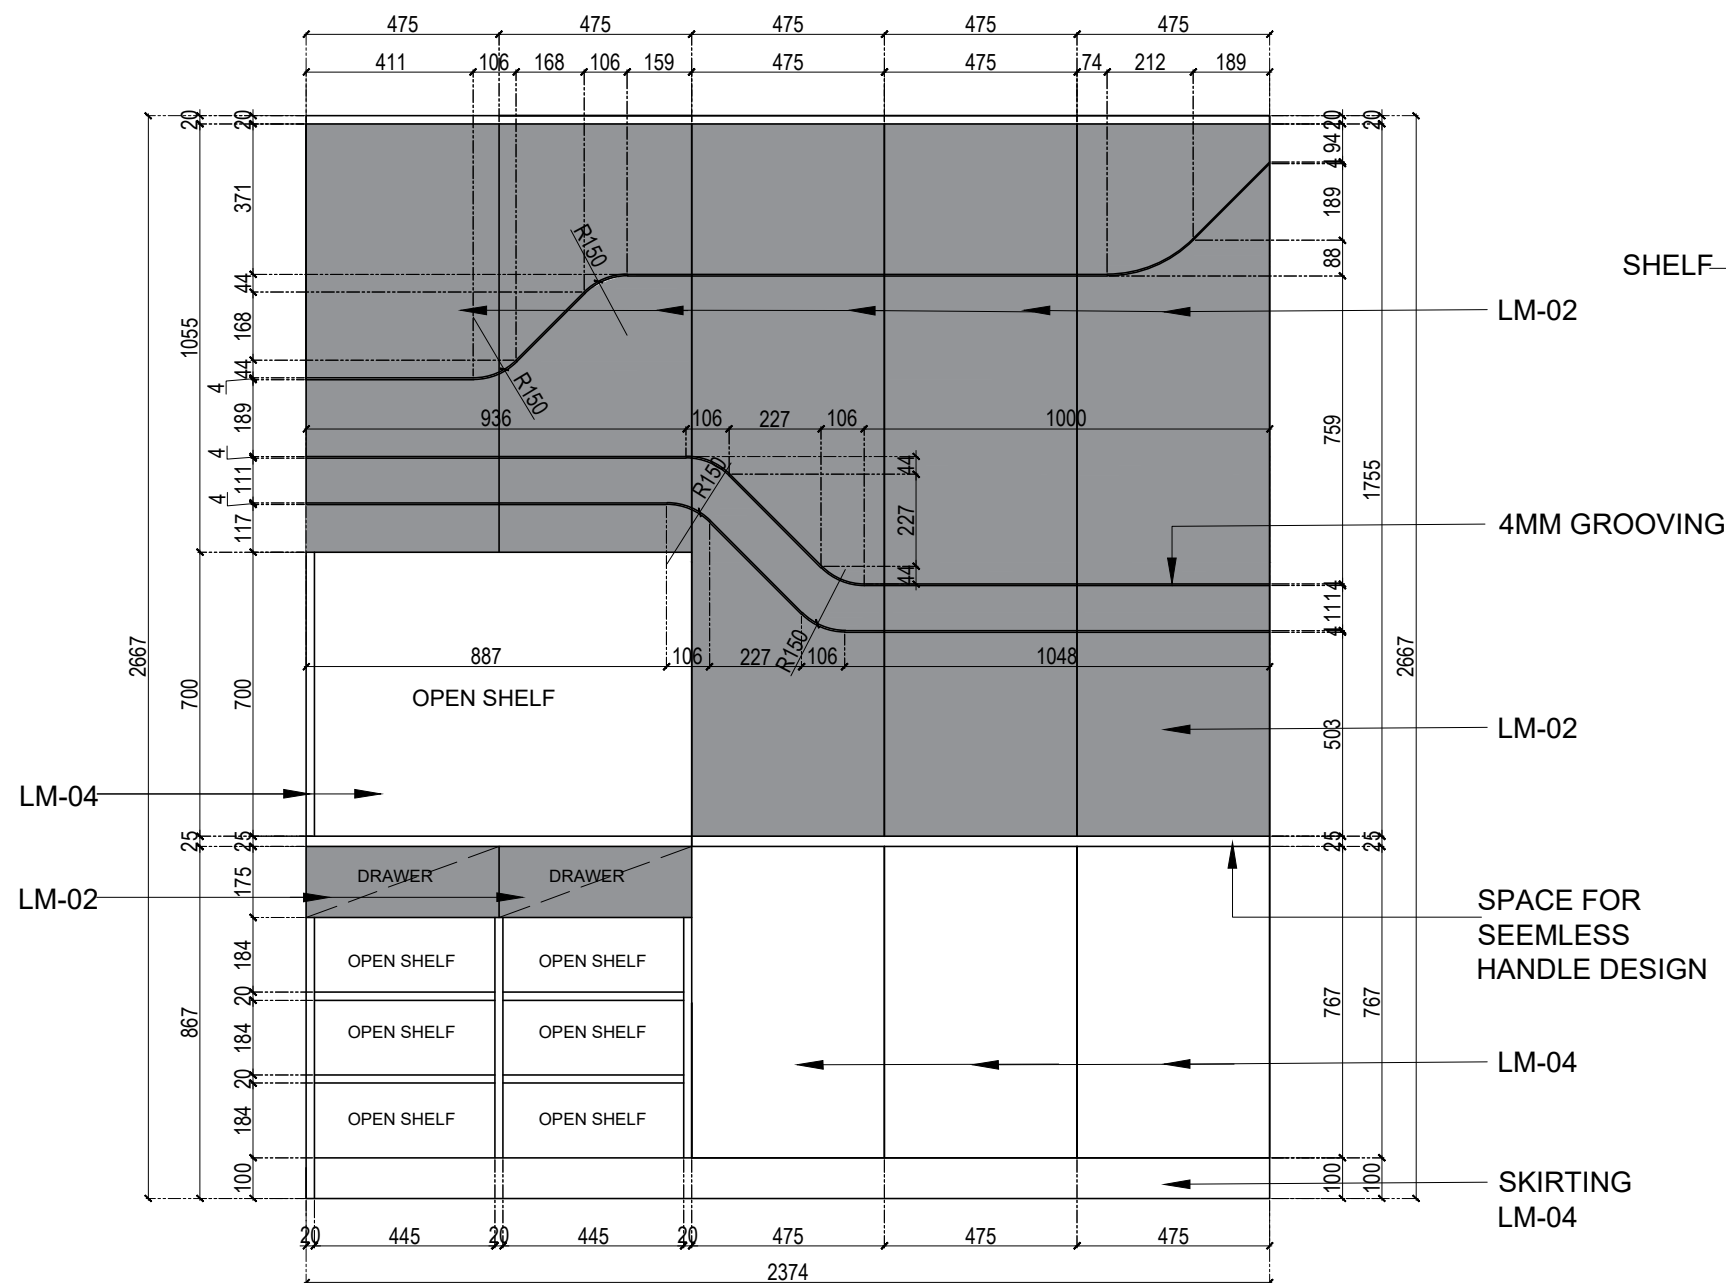


2 FRONT ELEVATION
WORKSTATION AREA

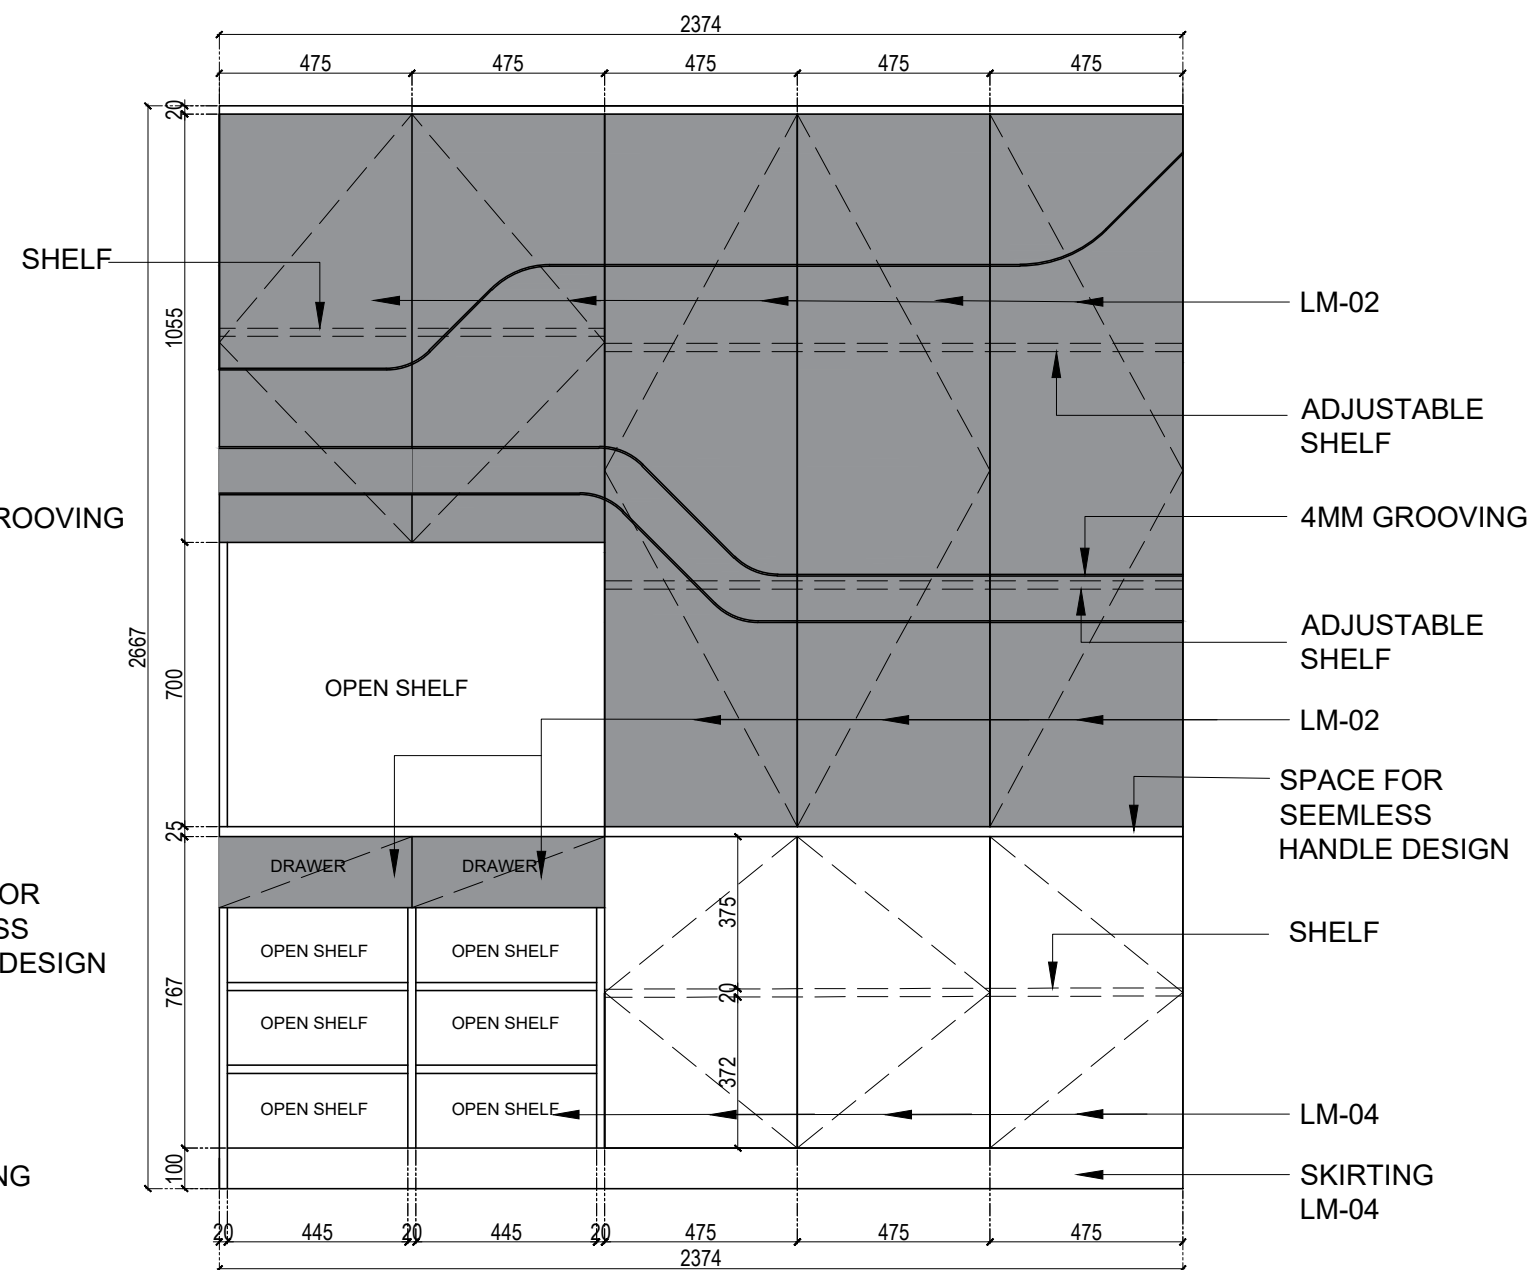


2.1 FRONT ELEVATION
WORKSTATION AREA


WORKSTATION AREA STORAGE

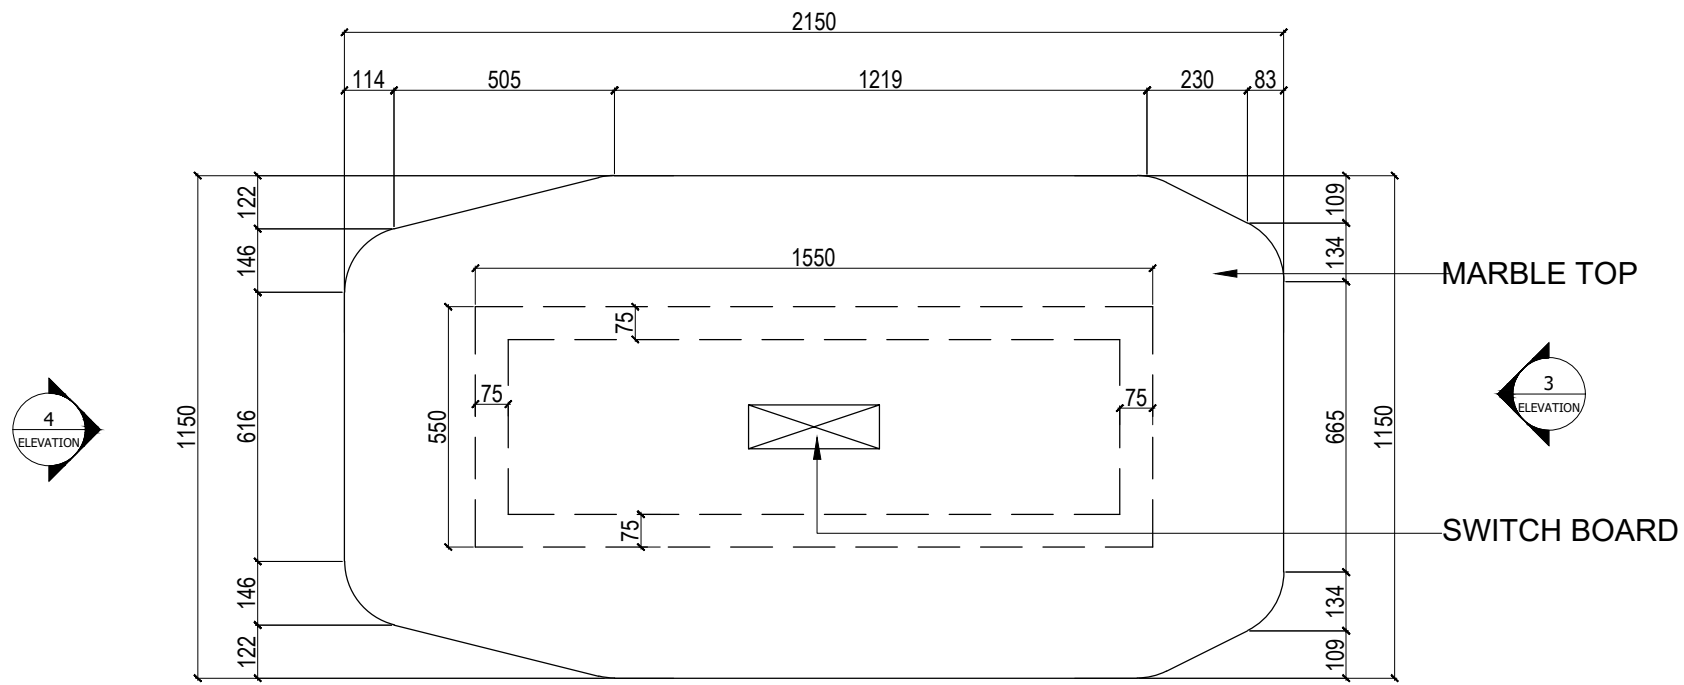


1 PLAN
MEETING TABLE

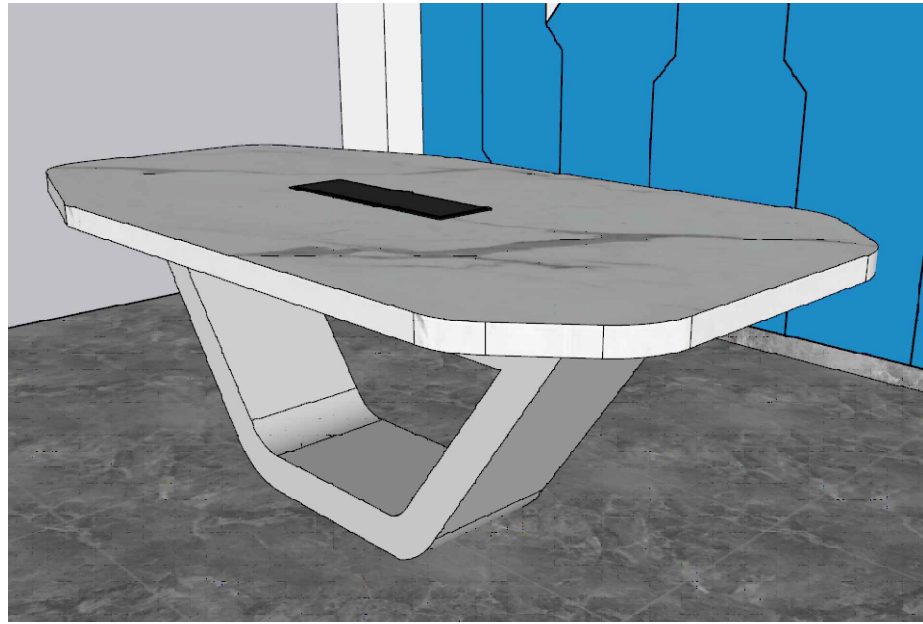


5 REFERENCE IMAGE
MEETING TABLE

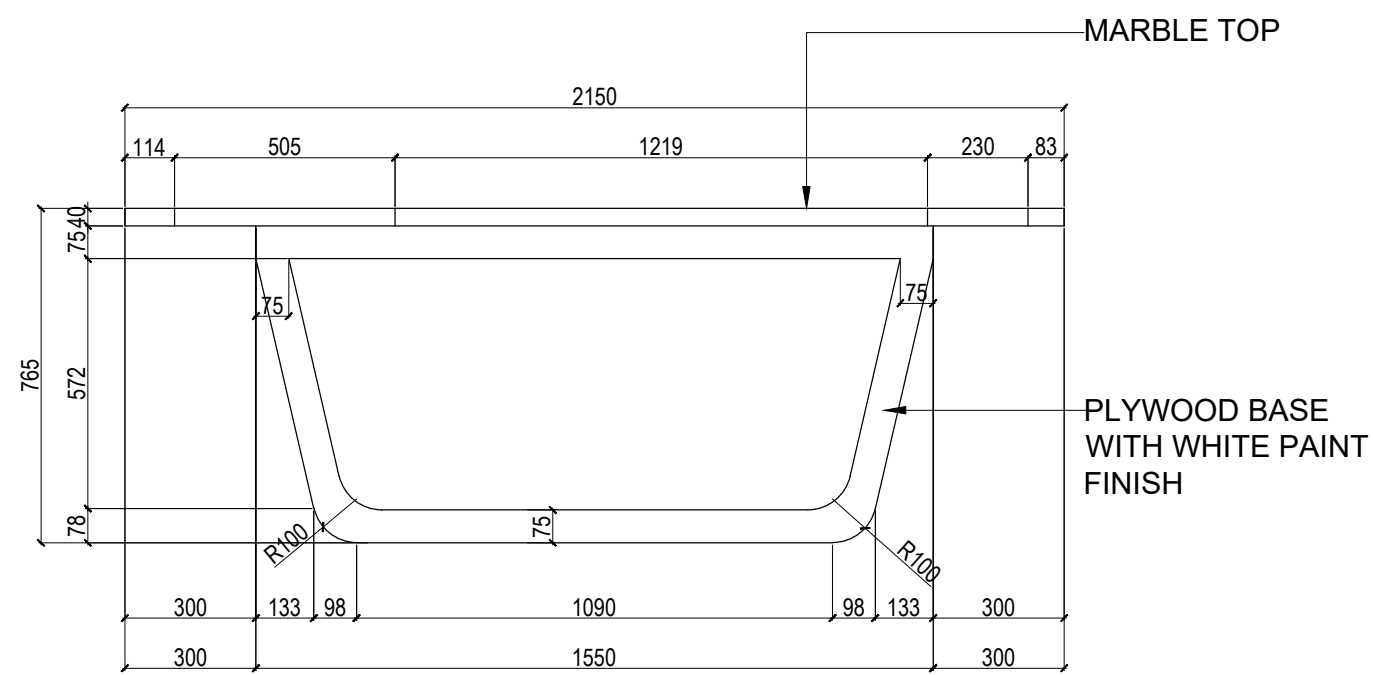

2 ELEVATION
MEETING TABLE

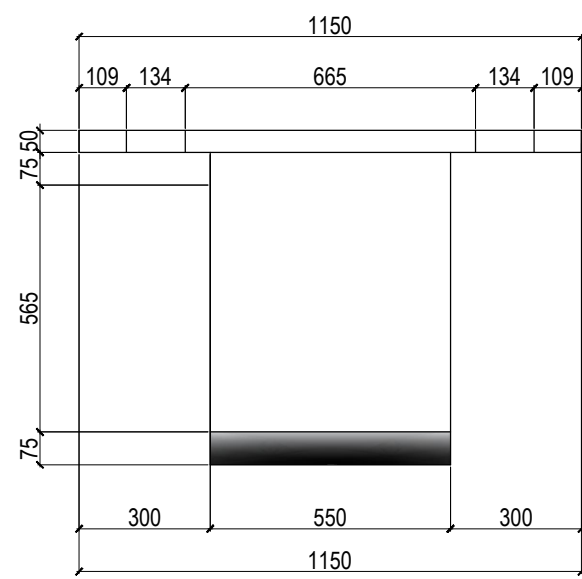


3 ELEVATION
MEETING TABLE

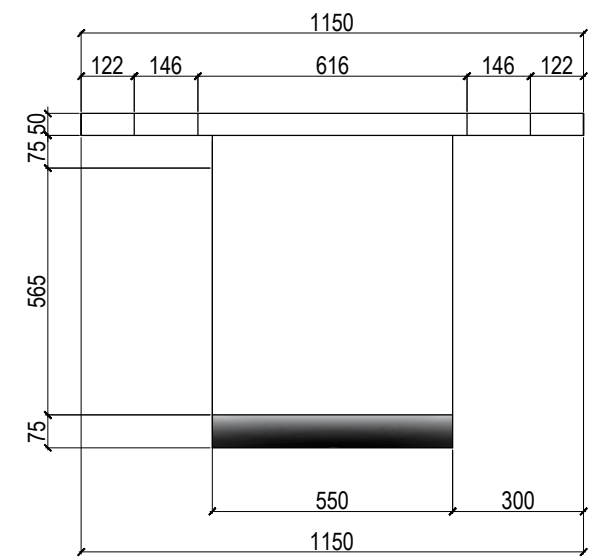


4 ELEVATION
MEETING TABLE

MEETING TABLE

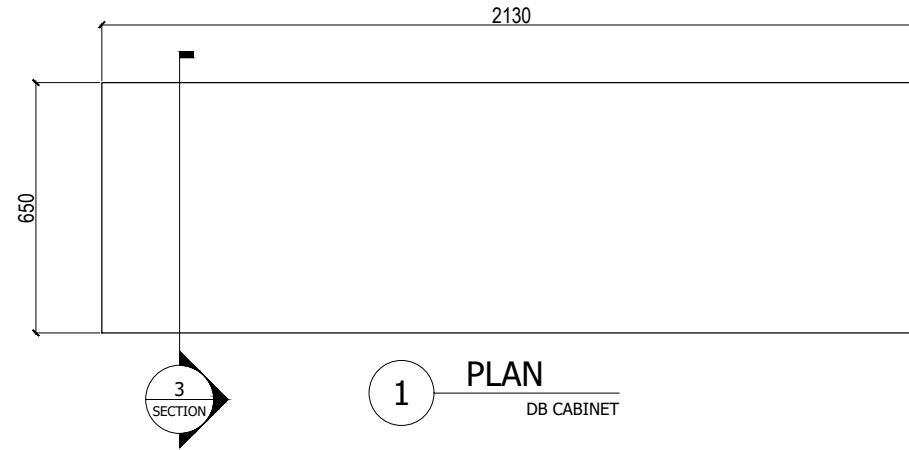


4 REFERENCE IMAGE

DB CABINET

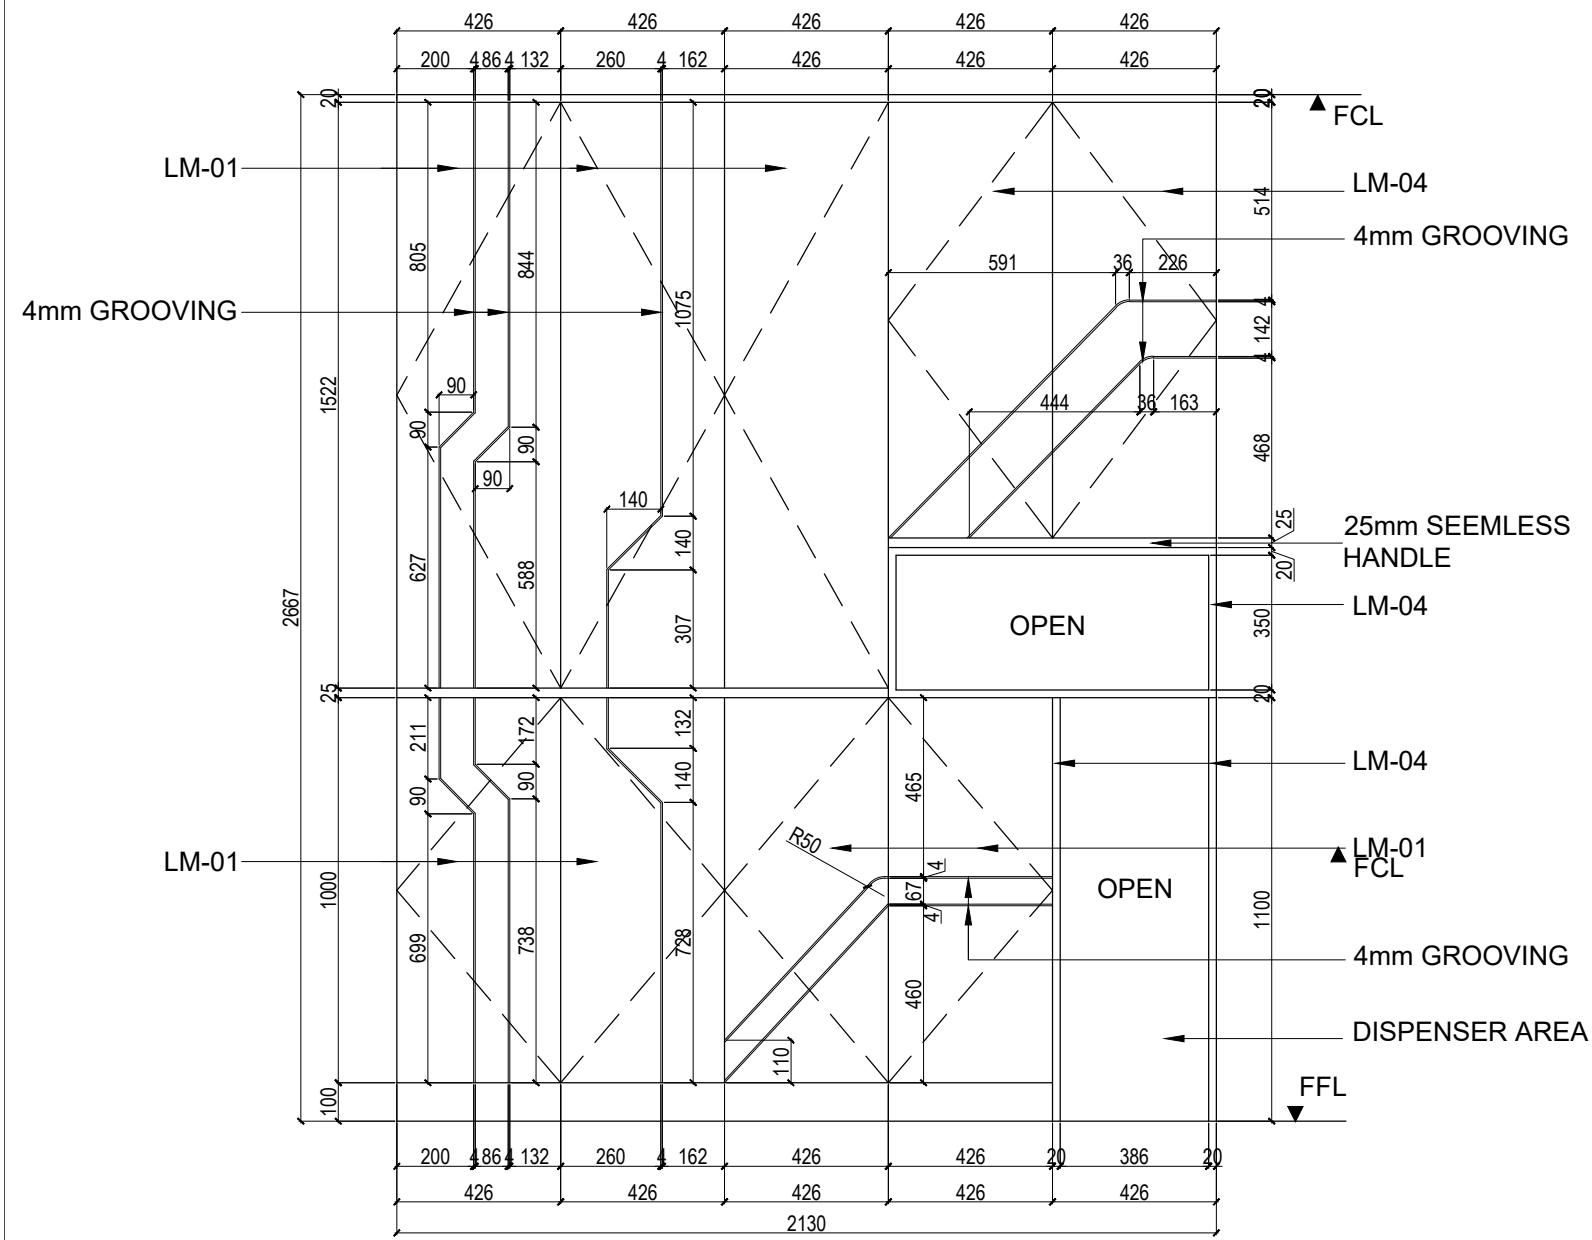

2 FRONT ELEVATION


DB CABINET

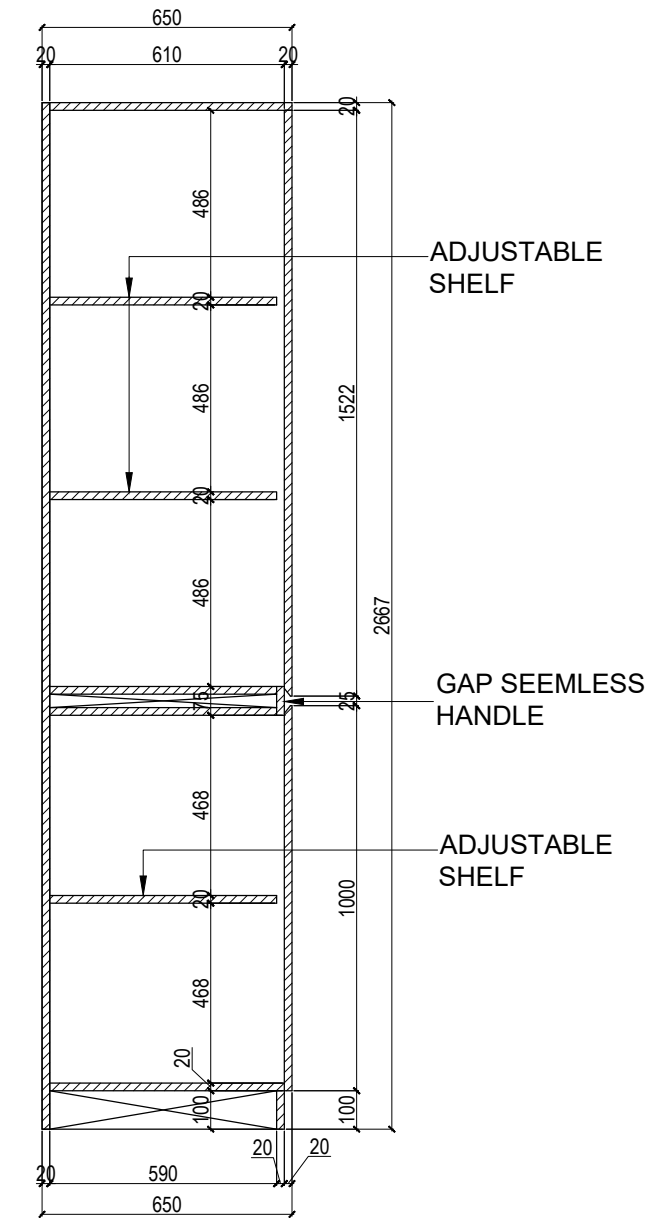


3 SECTION

DB CABINET


DB CABINET

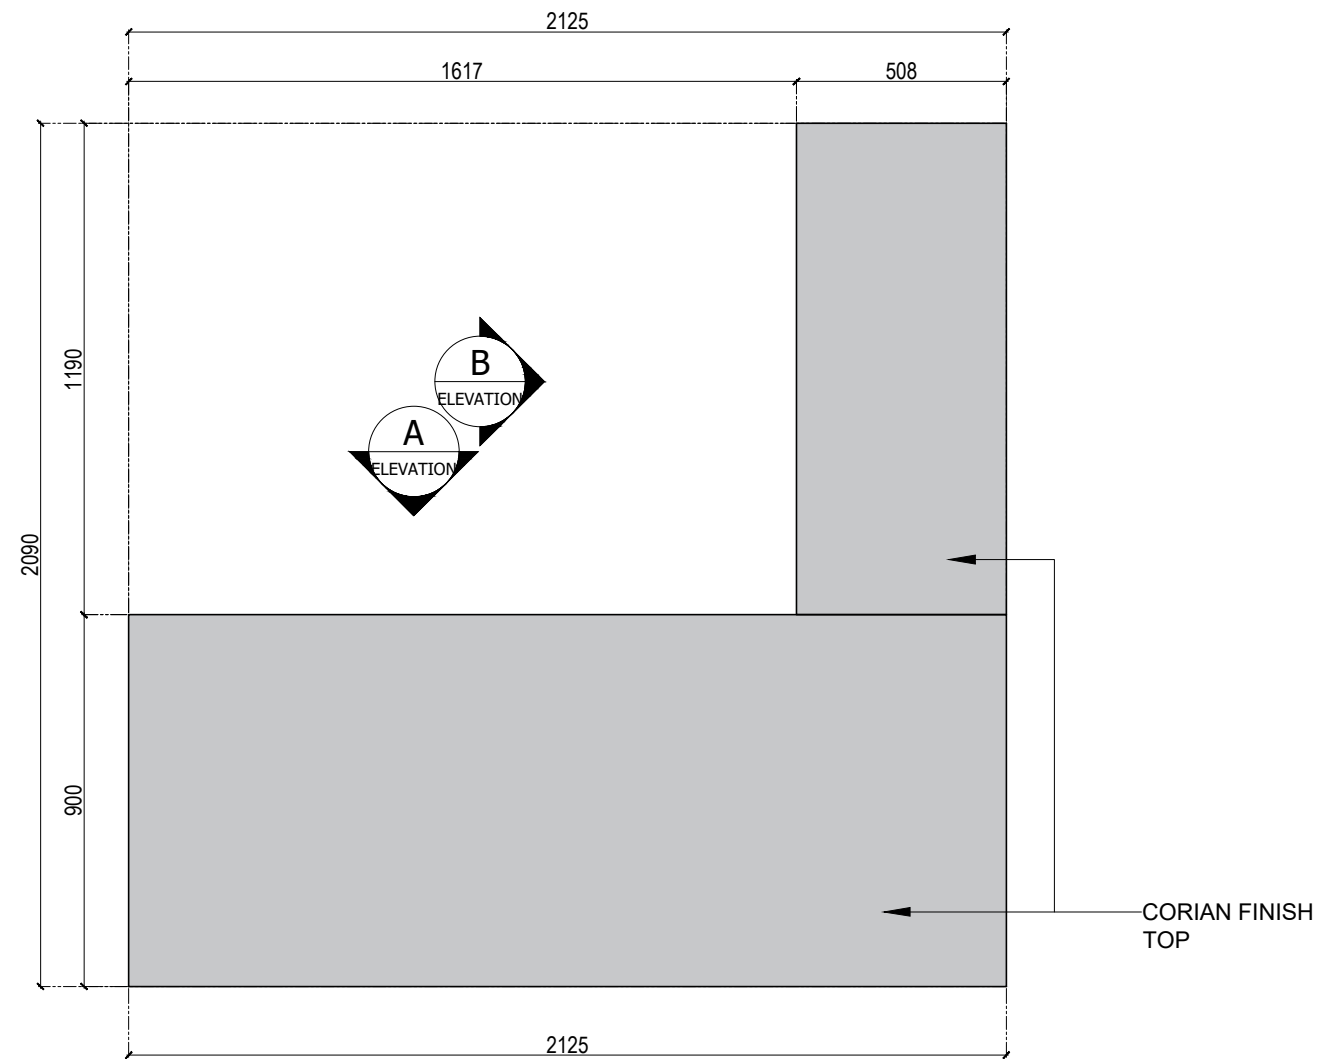


1 PLAN
MD WORKING TABLE

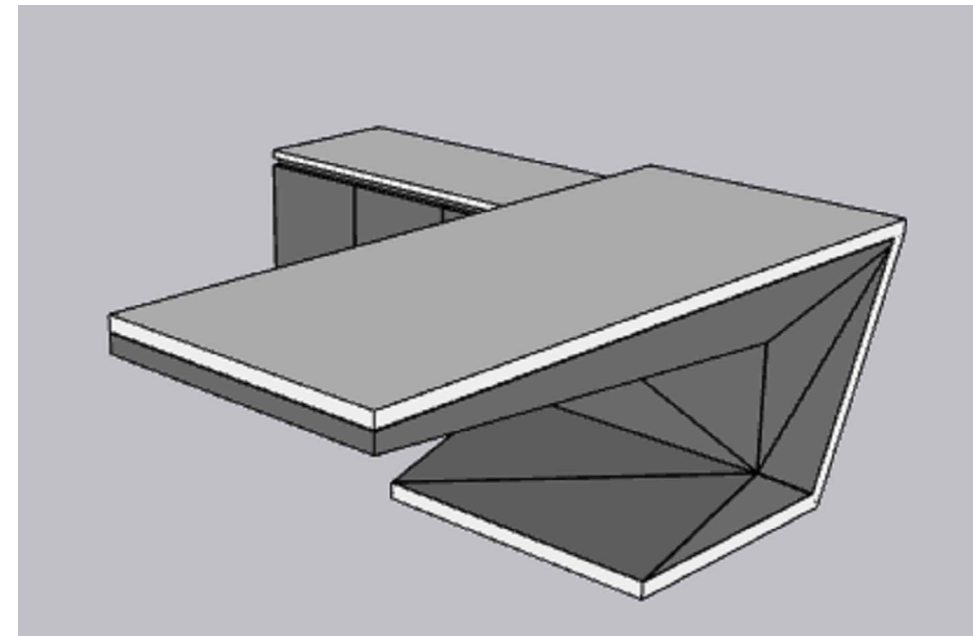

4 REFERENCE IMAGE
MD WORKING TABLE

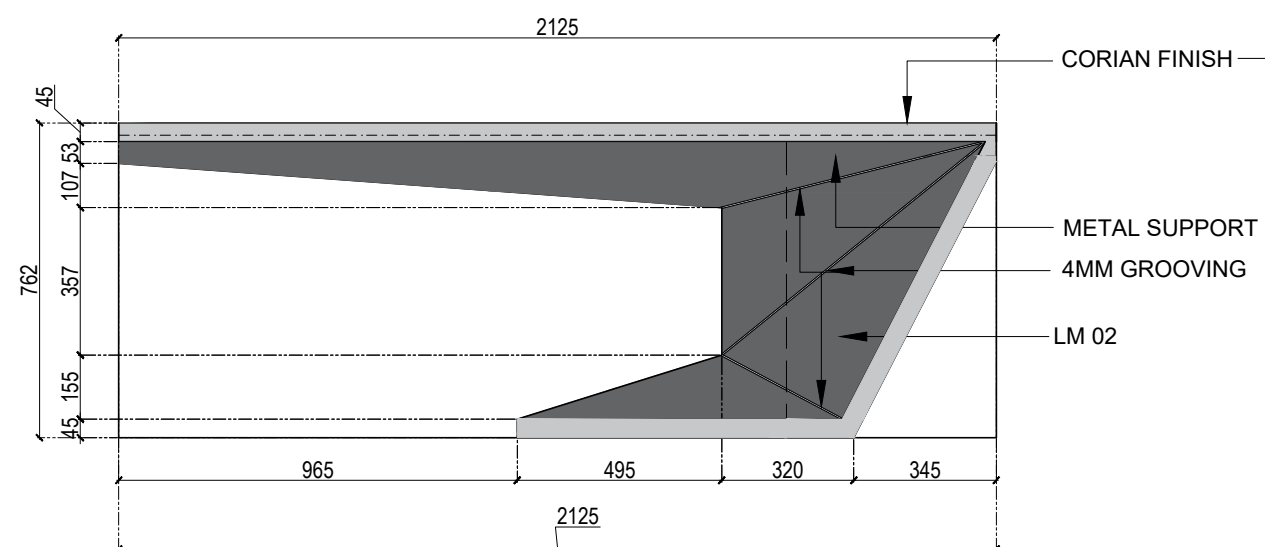


2 ELEVATION AT A
MD WORKING TABLE

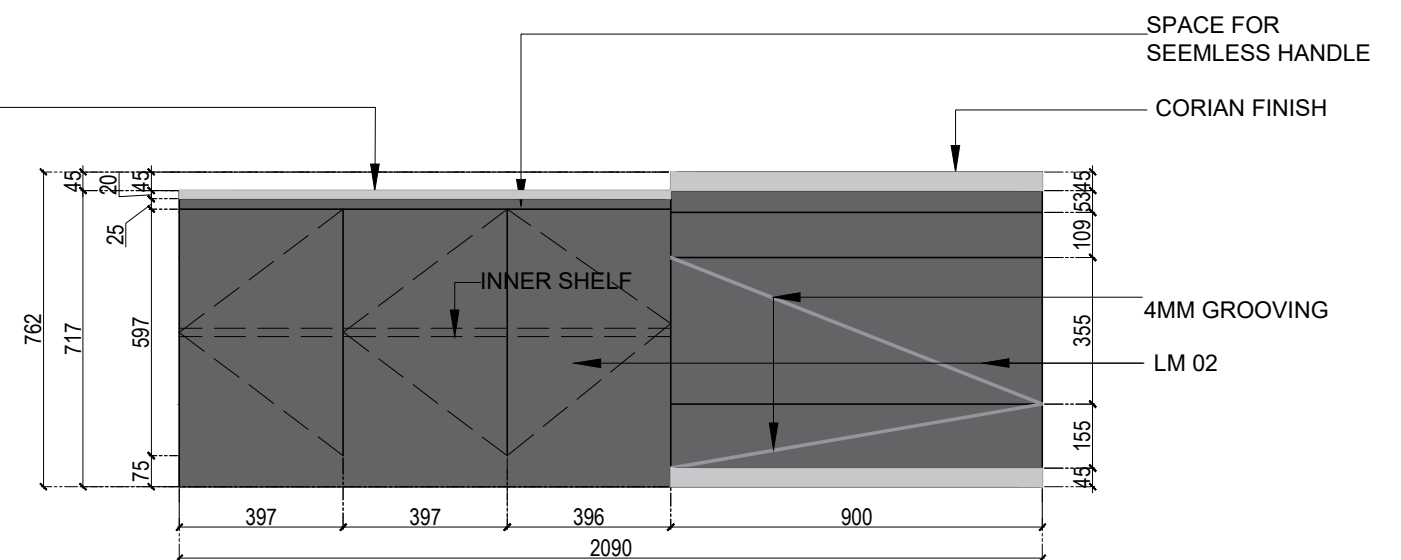


3 ELEVATION AT B
MD WORKING TABLE


MD WORKING TABLE

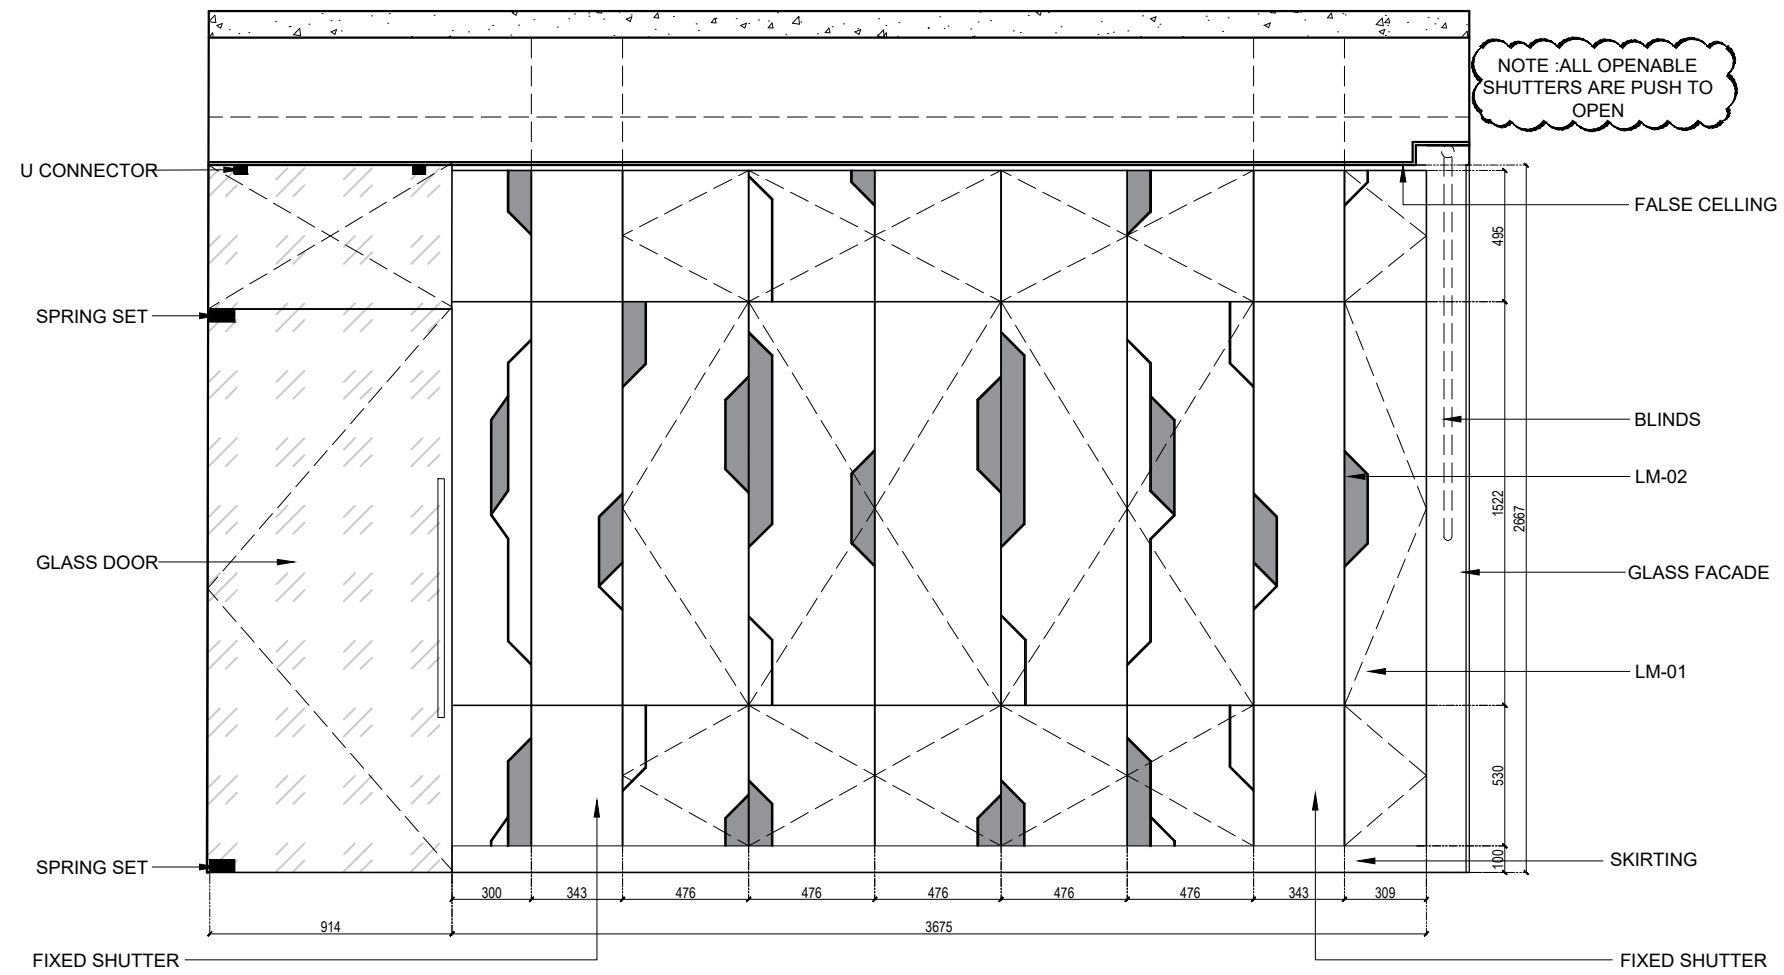


2.1 FRONT ELEVATION
MD STORAGE CABINETE

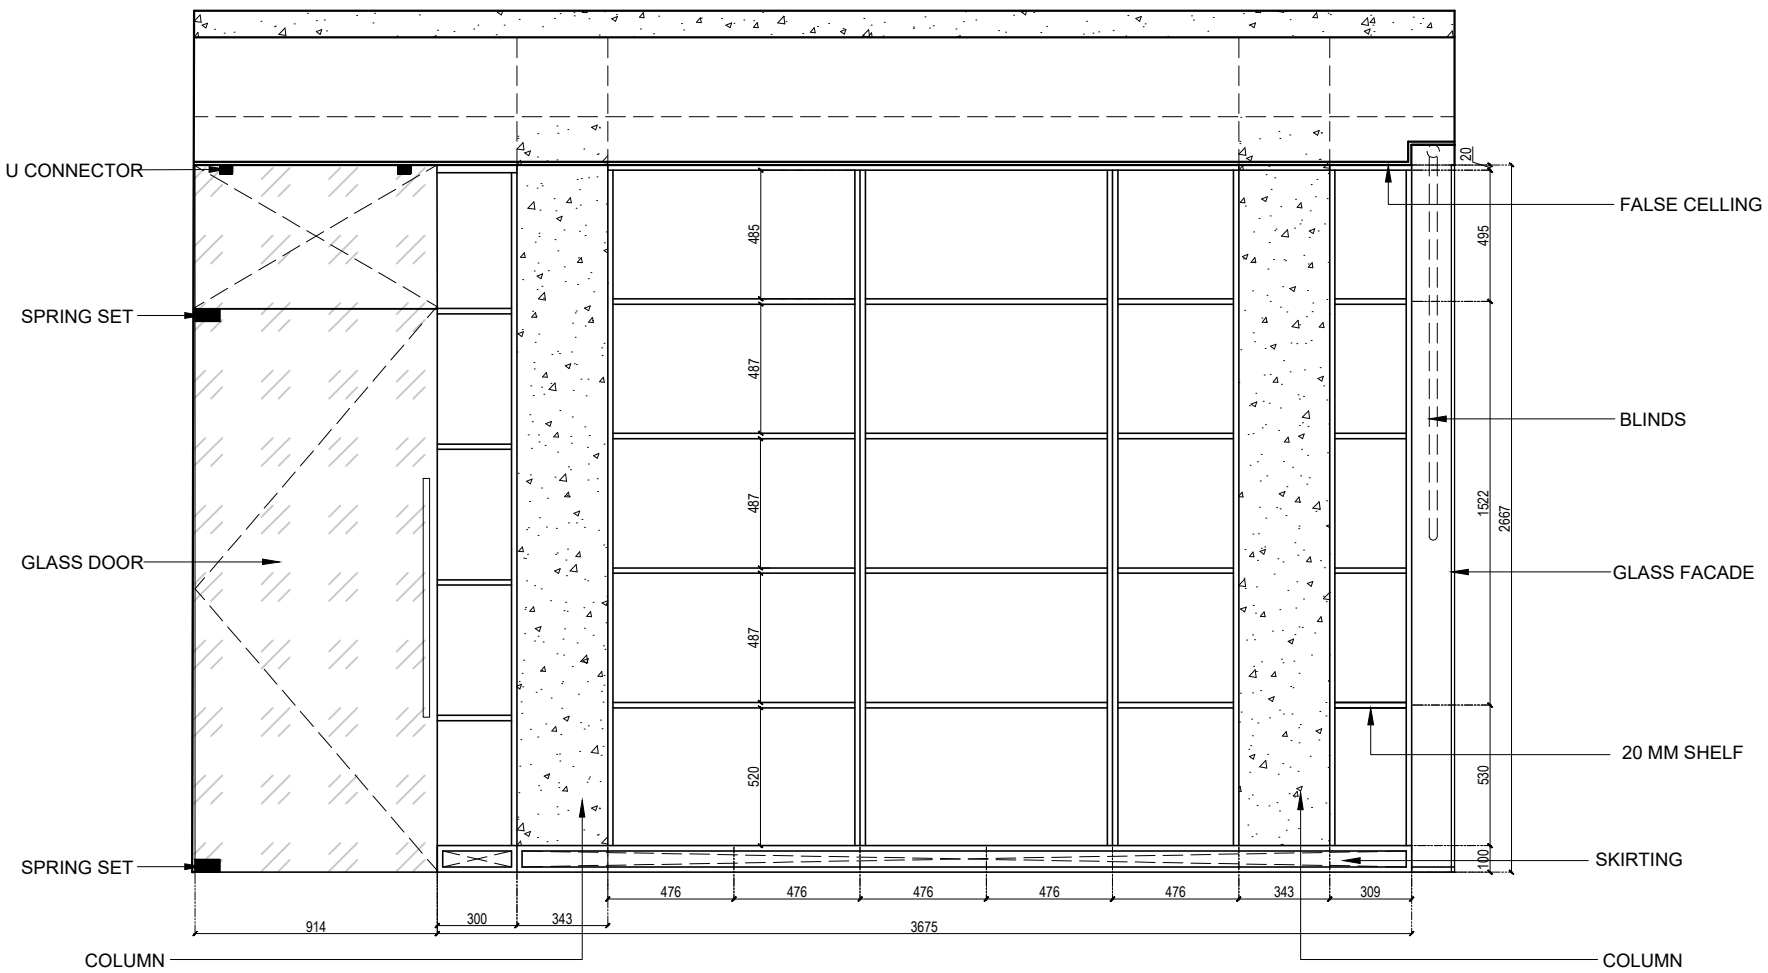


4 INNER ELEVATION
MD STORAGE CABINETE

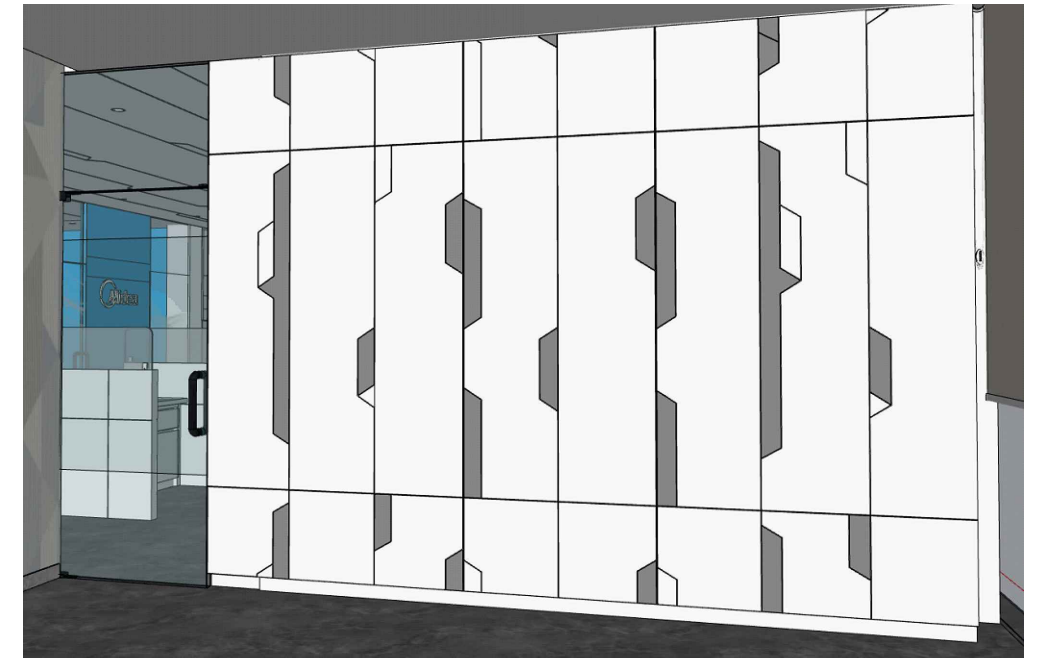


5 REFERENCE IMAGE
MD STORAGE CABINETE

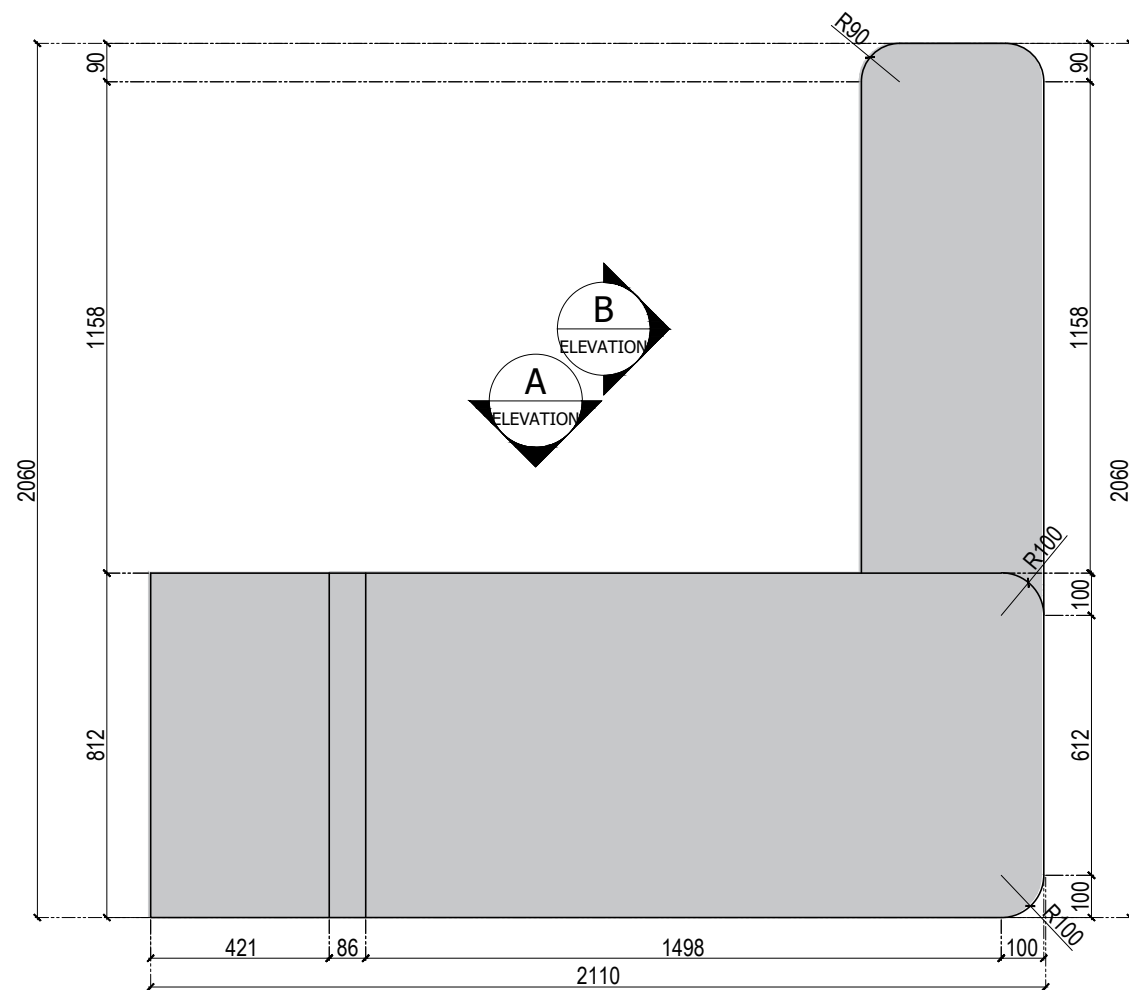


1 PLAN
DIRECTOR ROOM

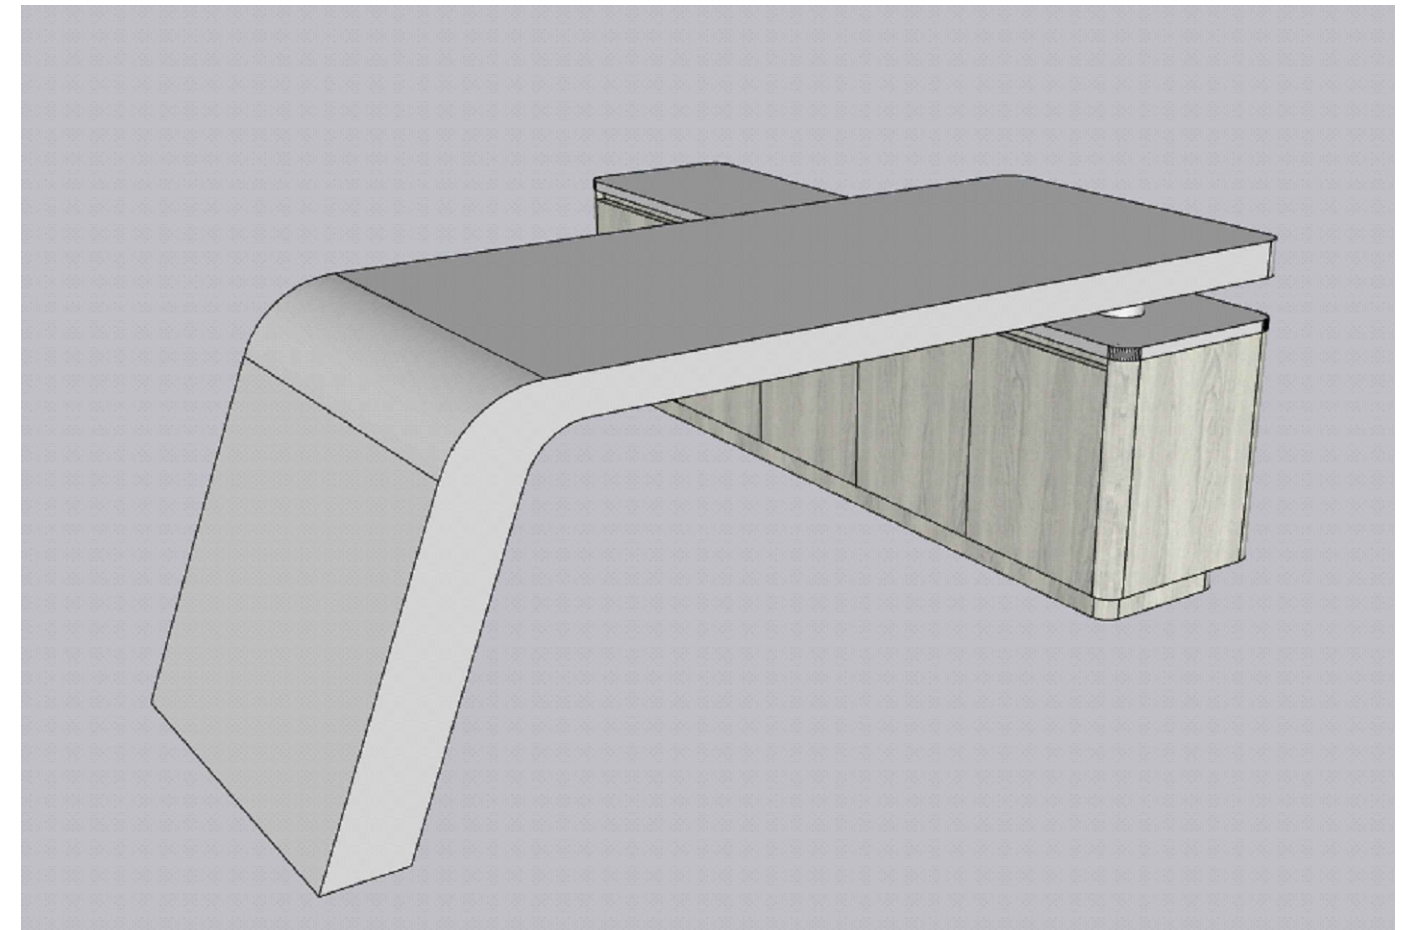

4 REFERENCE IMAGE
DIRECTOR ROOM

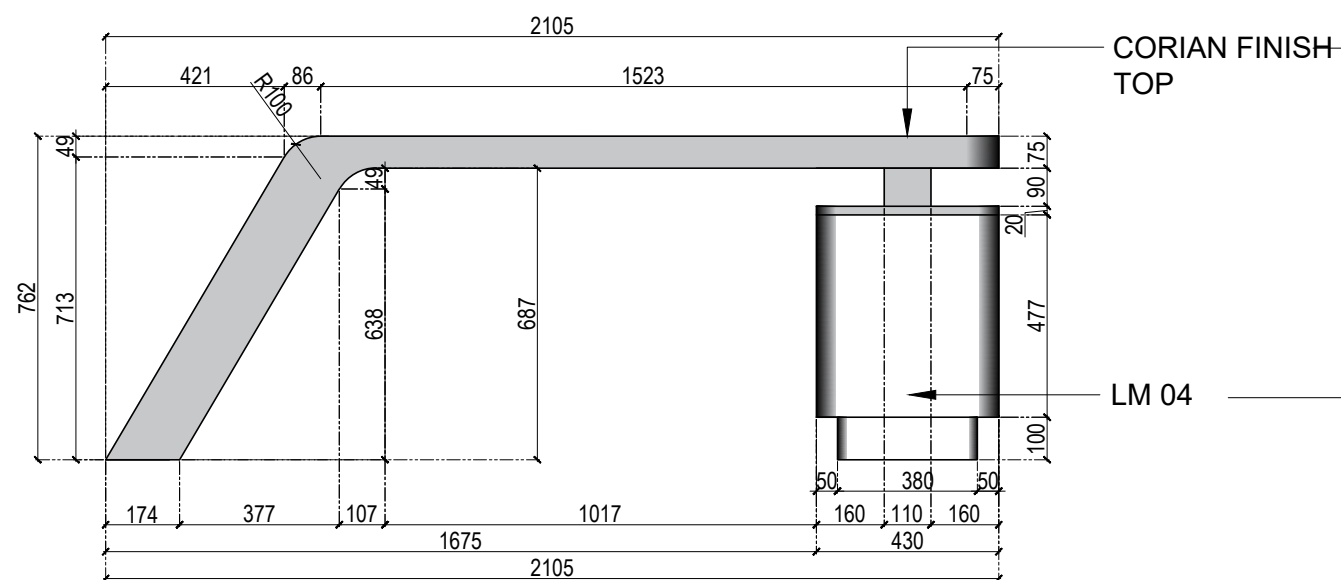


2 ELEVATION AT A
DIRECTOR ROOM


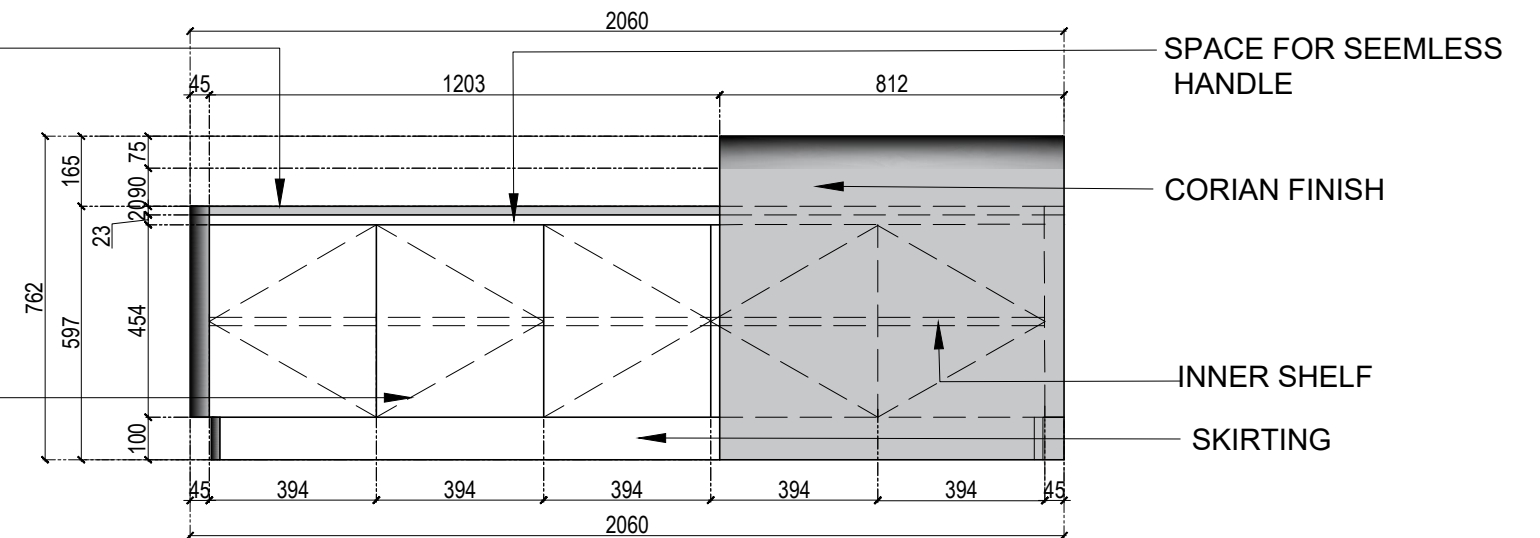


3 ELEVATION AT B
DIRECTOR ROOM


DIRECTOR WORKING TABLE

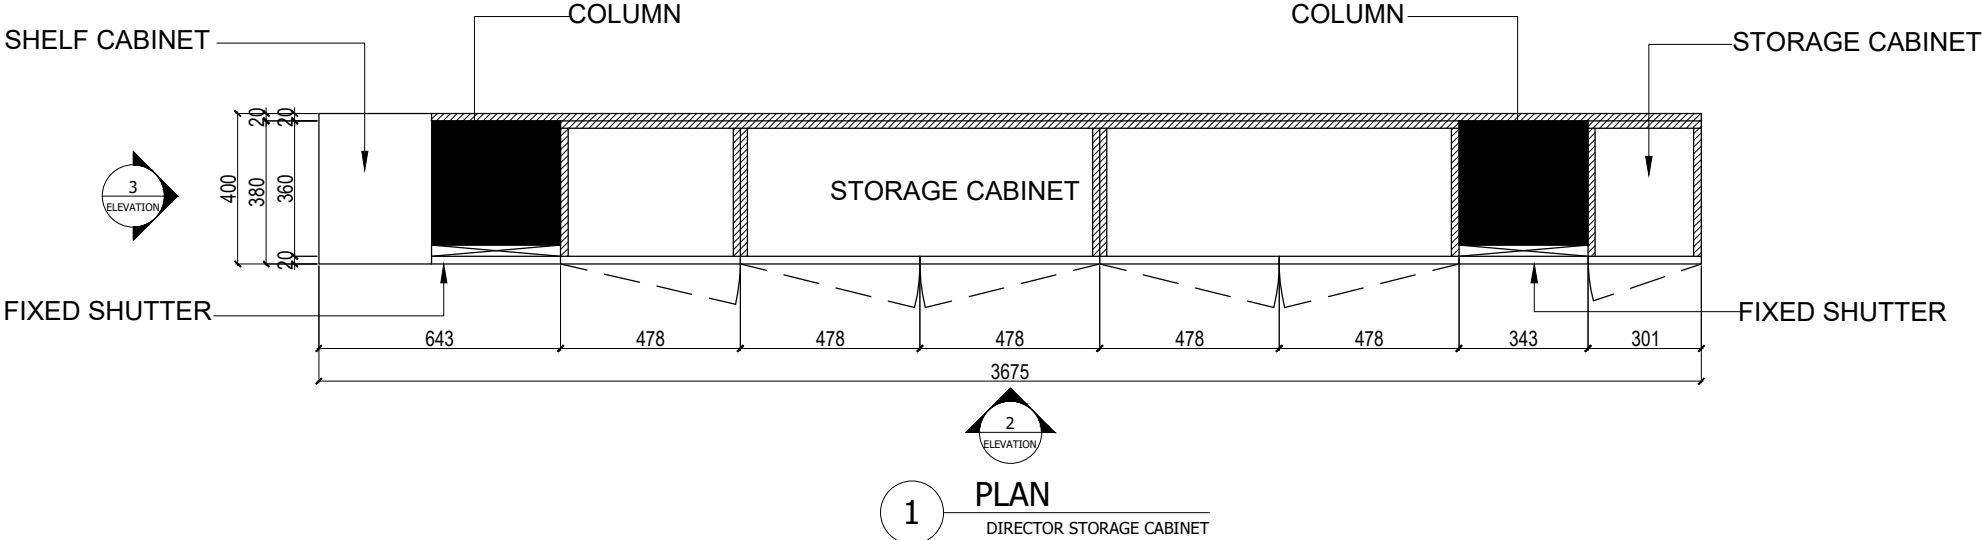


4 REFERENCE IMAGE
DIRECTOR STORAGE CABINET

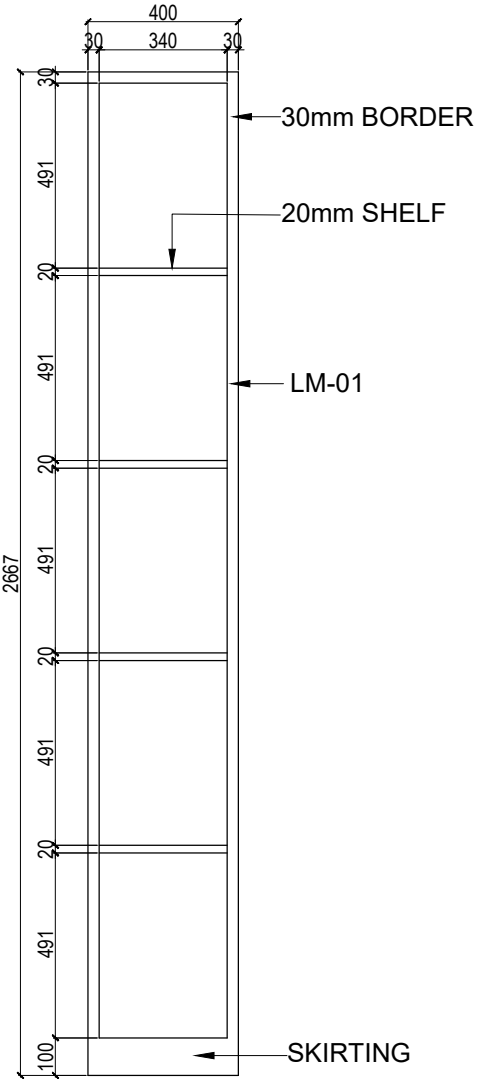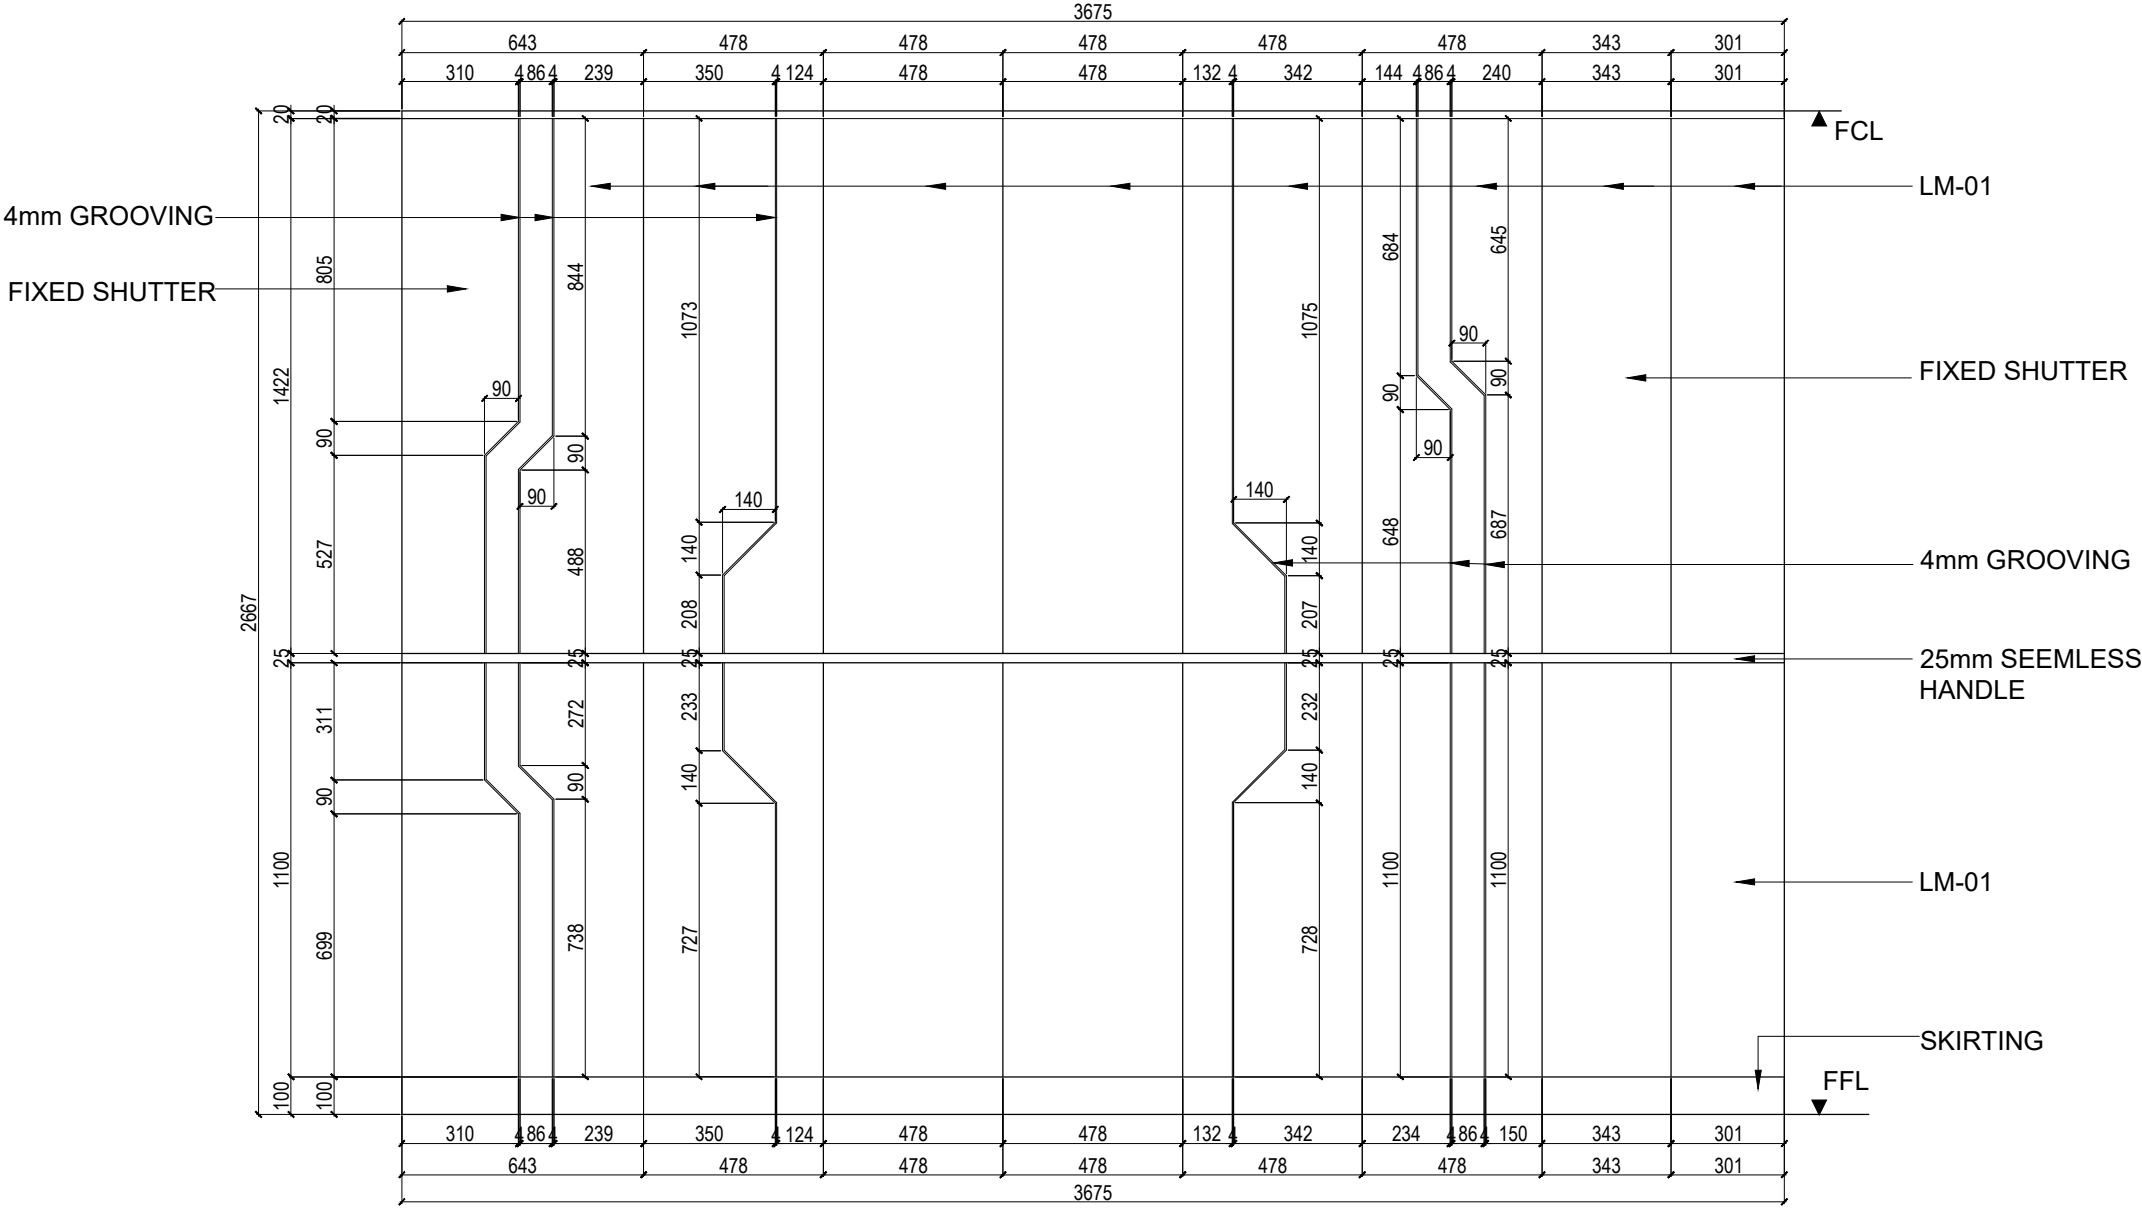


3 ELEVATION
DIRECTOR STORAGE CABINET

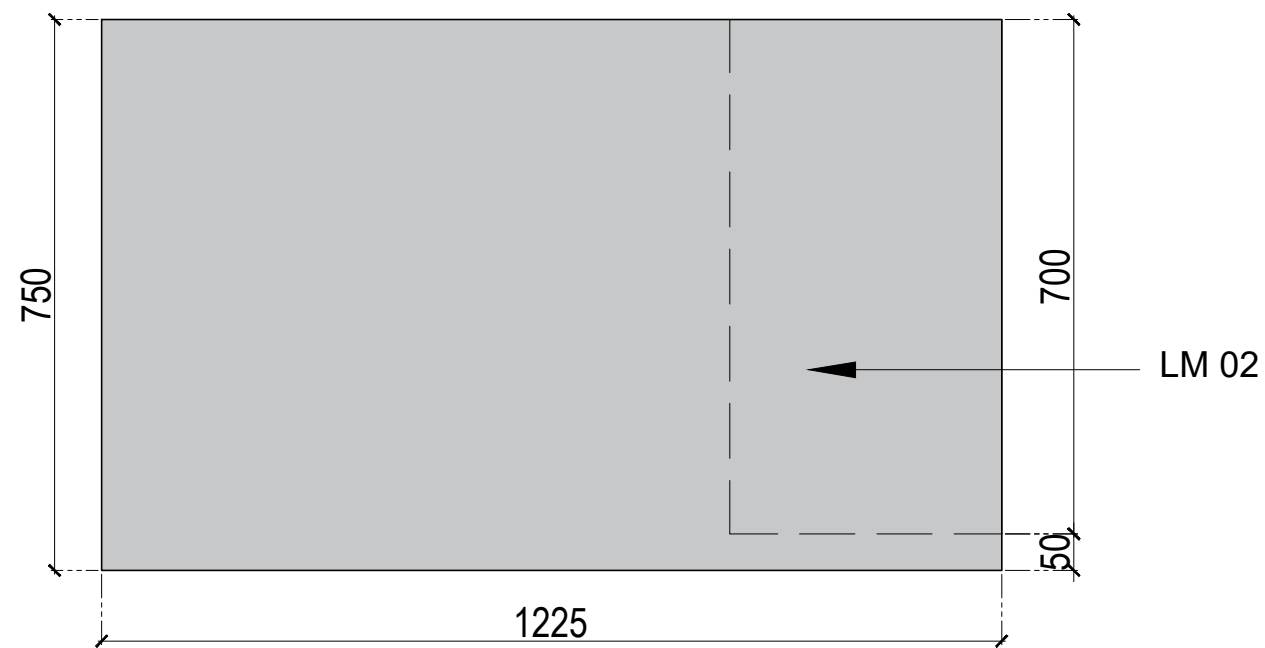


1 PLAN
WORK STATION

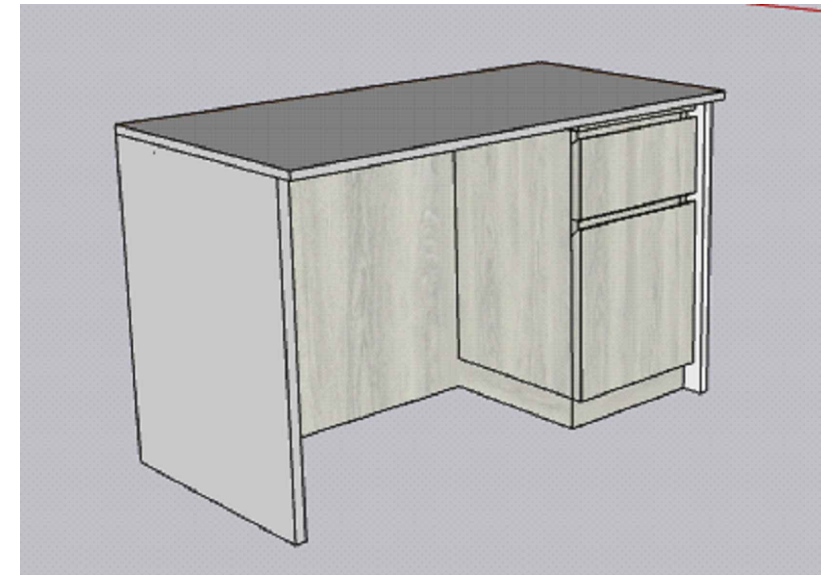

4 REFERENCE IMAGE
WORK STATION

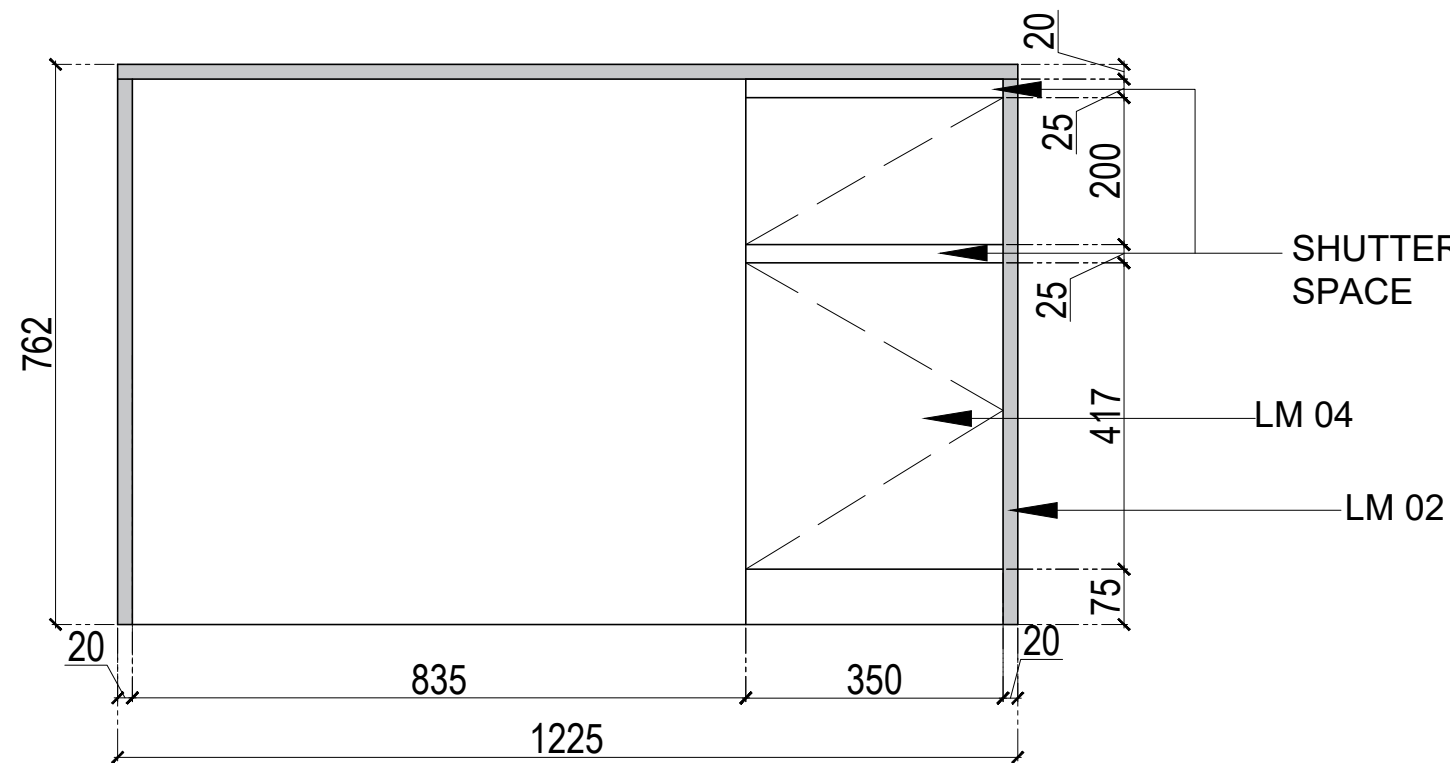


2 FRONT ELEVATION
WORK STATION

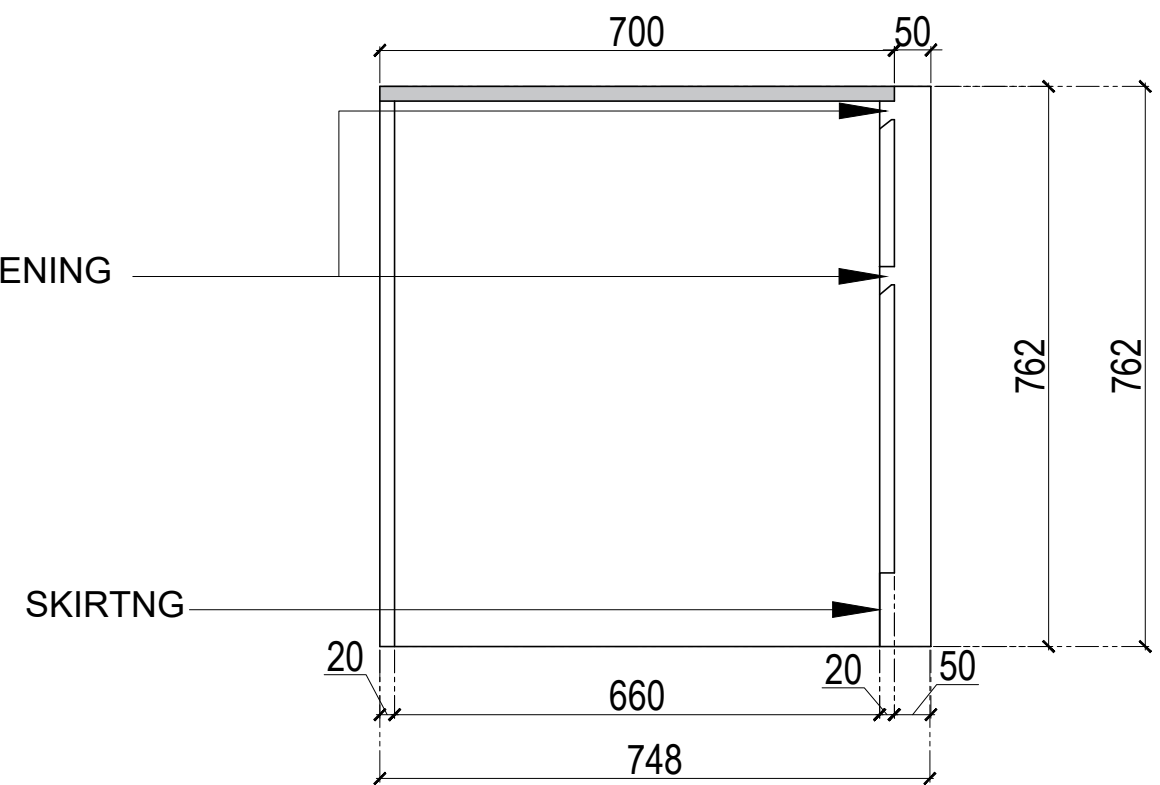


3 SIDE ELEVATION
WORK STATION


WORK STATION AREA WORK STATION

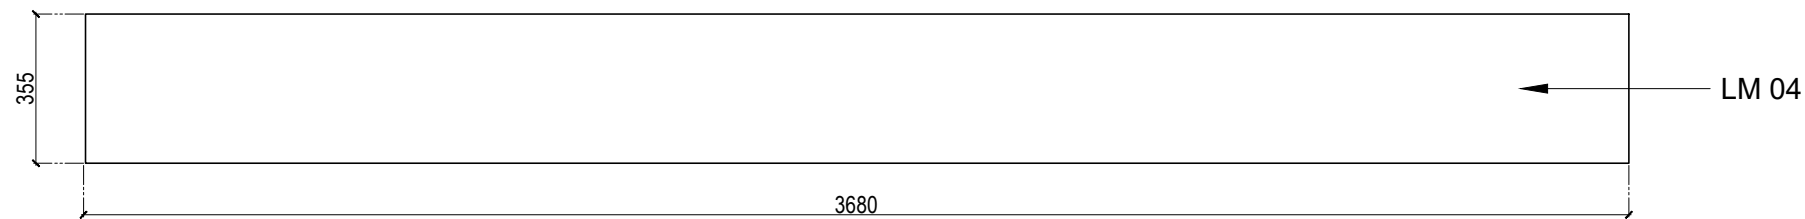

1 PLAN
UPPERHEAD CABINATE

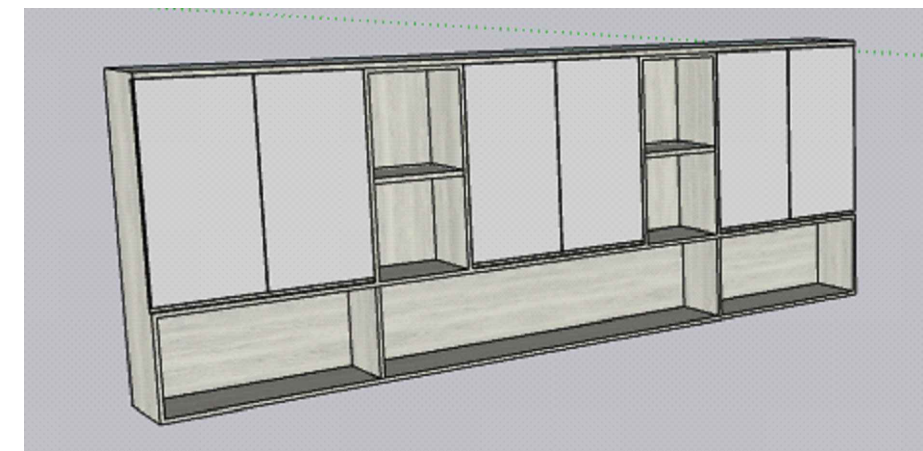

4 REFERENCE IMAGE
UPPERHEAD CABINATE

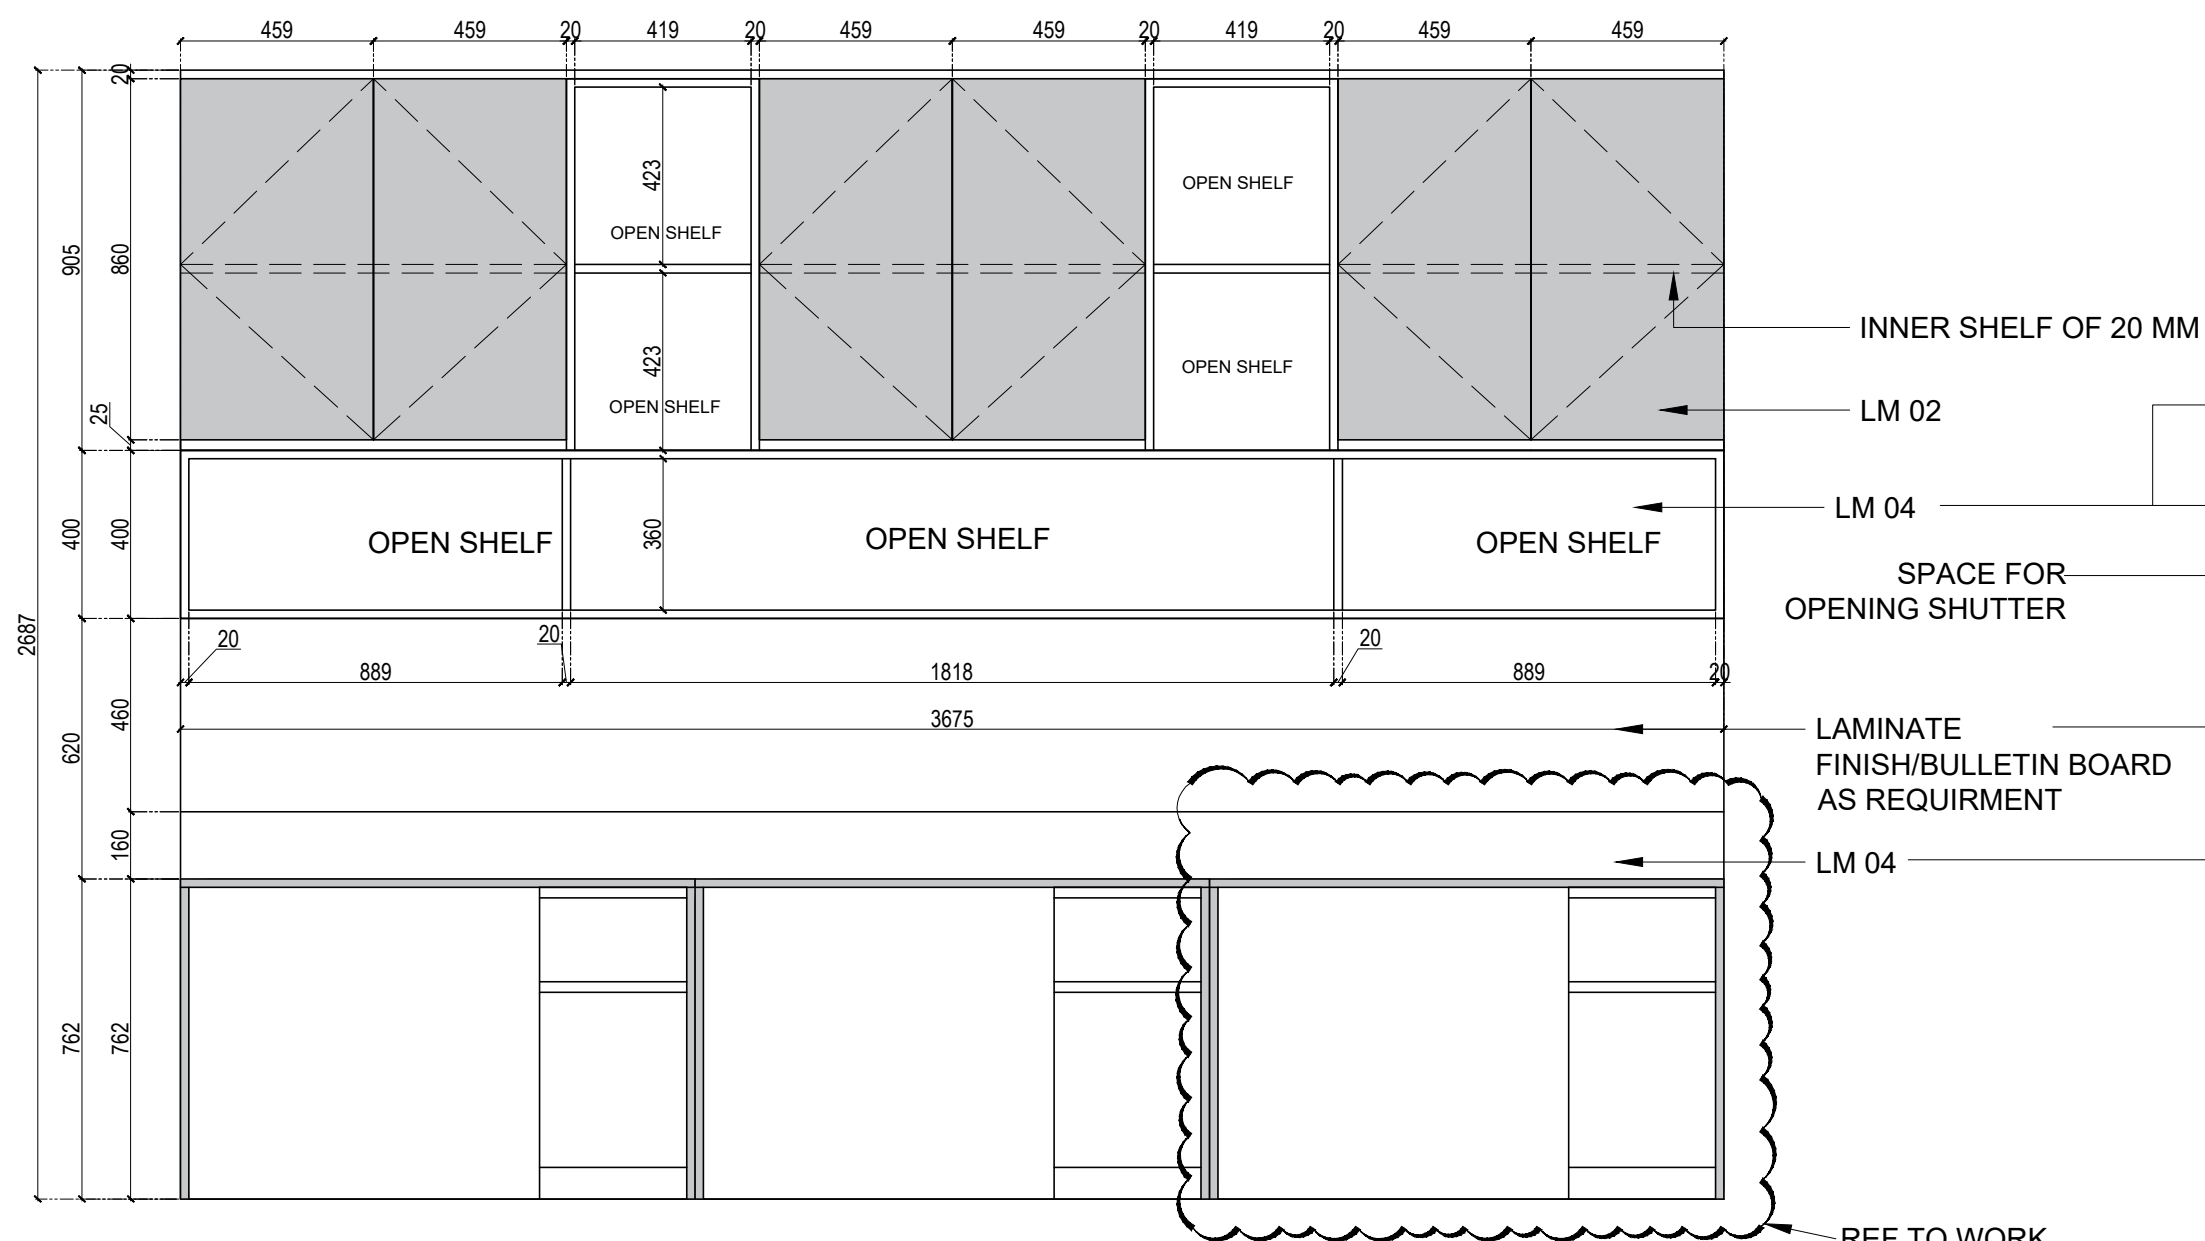


2 FRONT ELEVATION
UPPERHEAD CABINATE

INNER SHELF OF 20 MM
LM 02
LM 04
SPACE FOR
OPENING SHUTTER



LAMINATE
FINISH/BULLETIN BOARD
AS REQUIRMENT
LM 04

REF TO WORK
STATION DETAIL

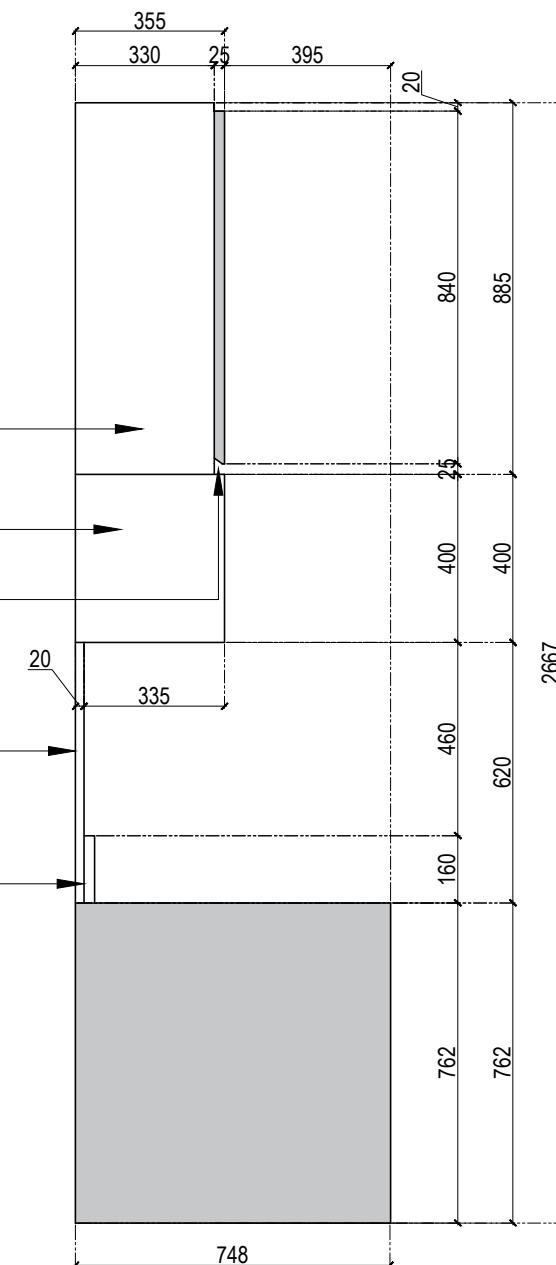

3 SIDE ELEVATION
UPPERHEAD CABINATE


WORK STATION AREA UPPER CABINATE

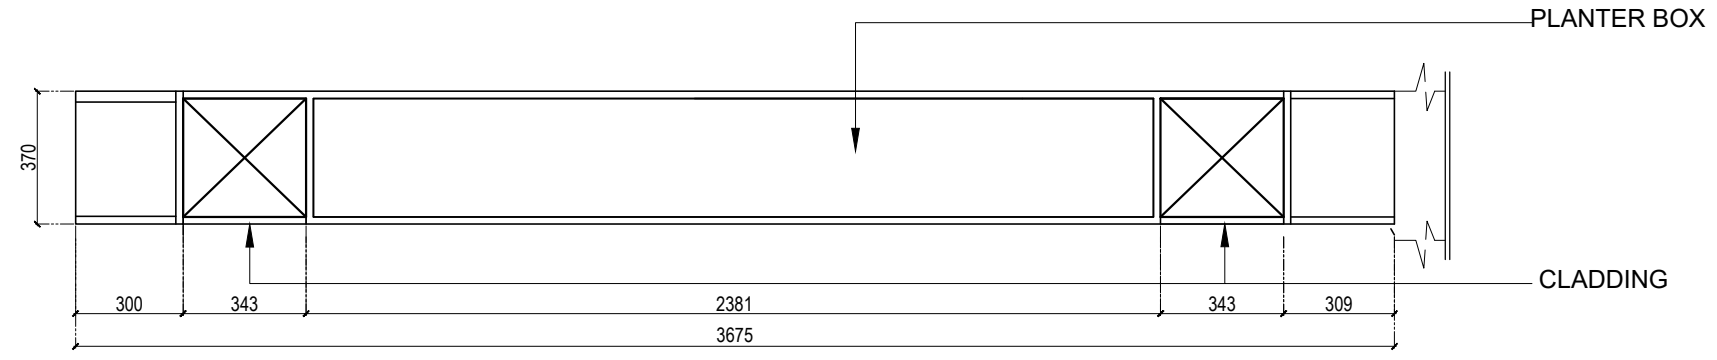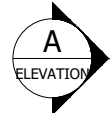

1 PLAN
WORKSTATION AREA PLANTER BOX



1 REFERENCE IMAGE
WORKSTATION AREA PLANTER BOX

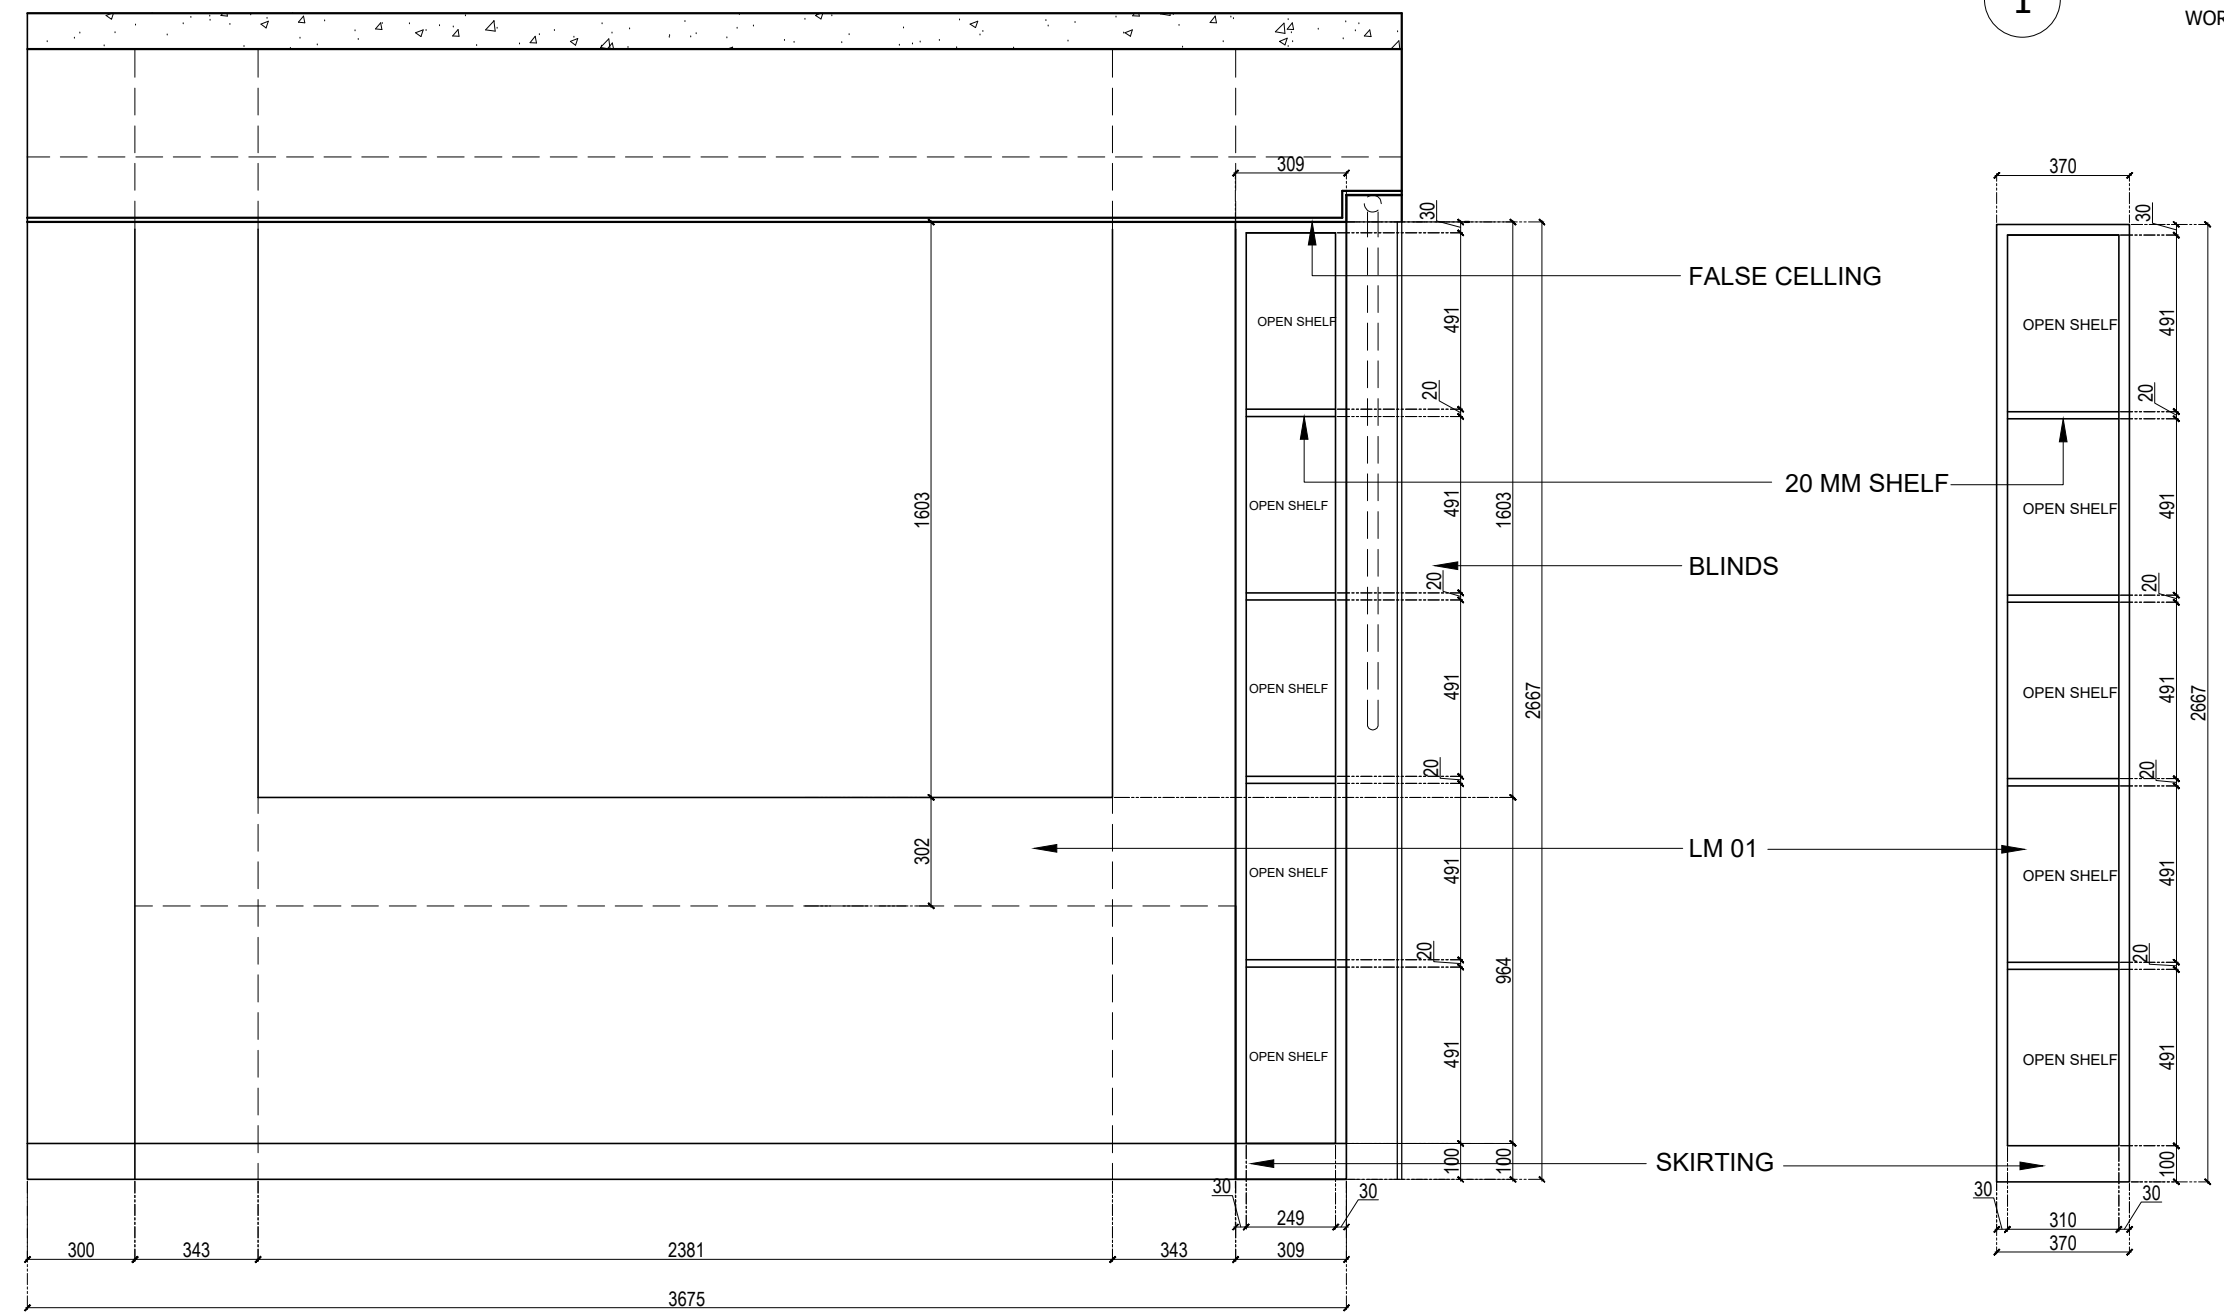

2.1 FRONT ELEVATION
WORKSTATION AREA PLANTER BOX

3 ELEVATION AT A
WORKSTATION AREA PLANTER BOX

WORKSTATION AREA PLANTER BOX