



FURNITURE DETAILS




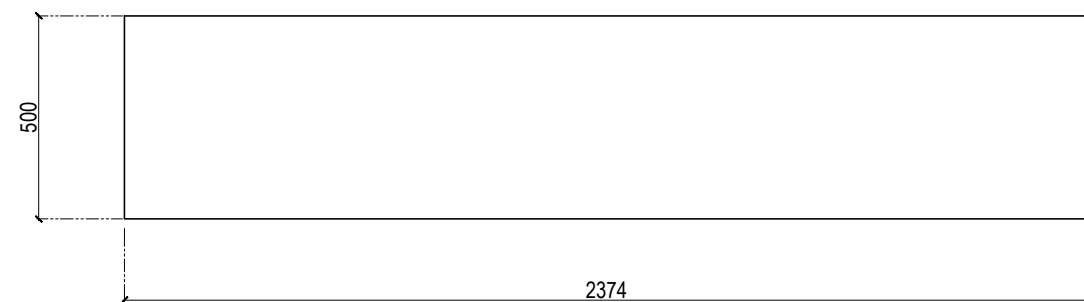


1 PLAN
WORKSTATION AREA STORAGE

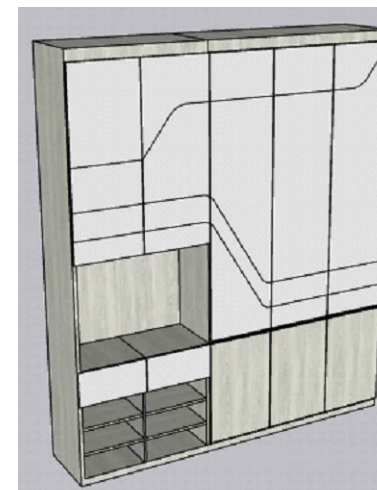

3 REFERENCE IMAGE
WORKSTATION AREA STORAGE



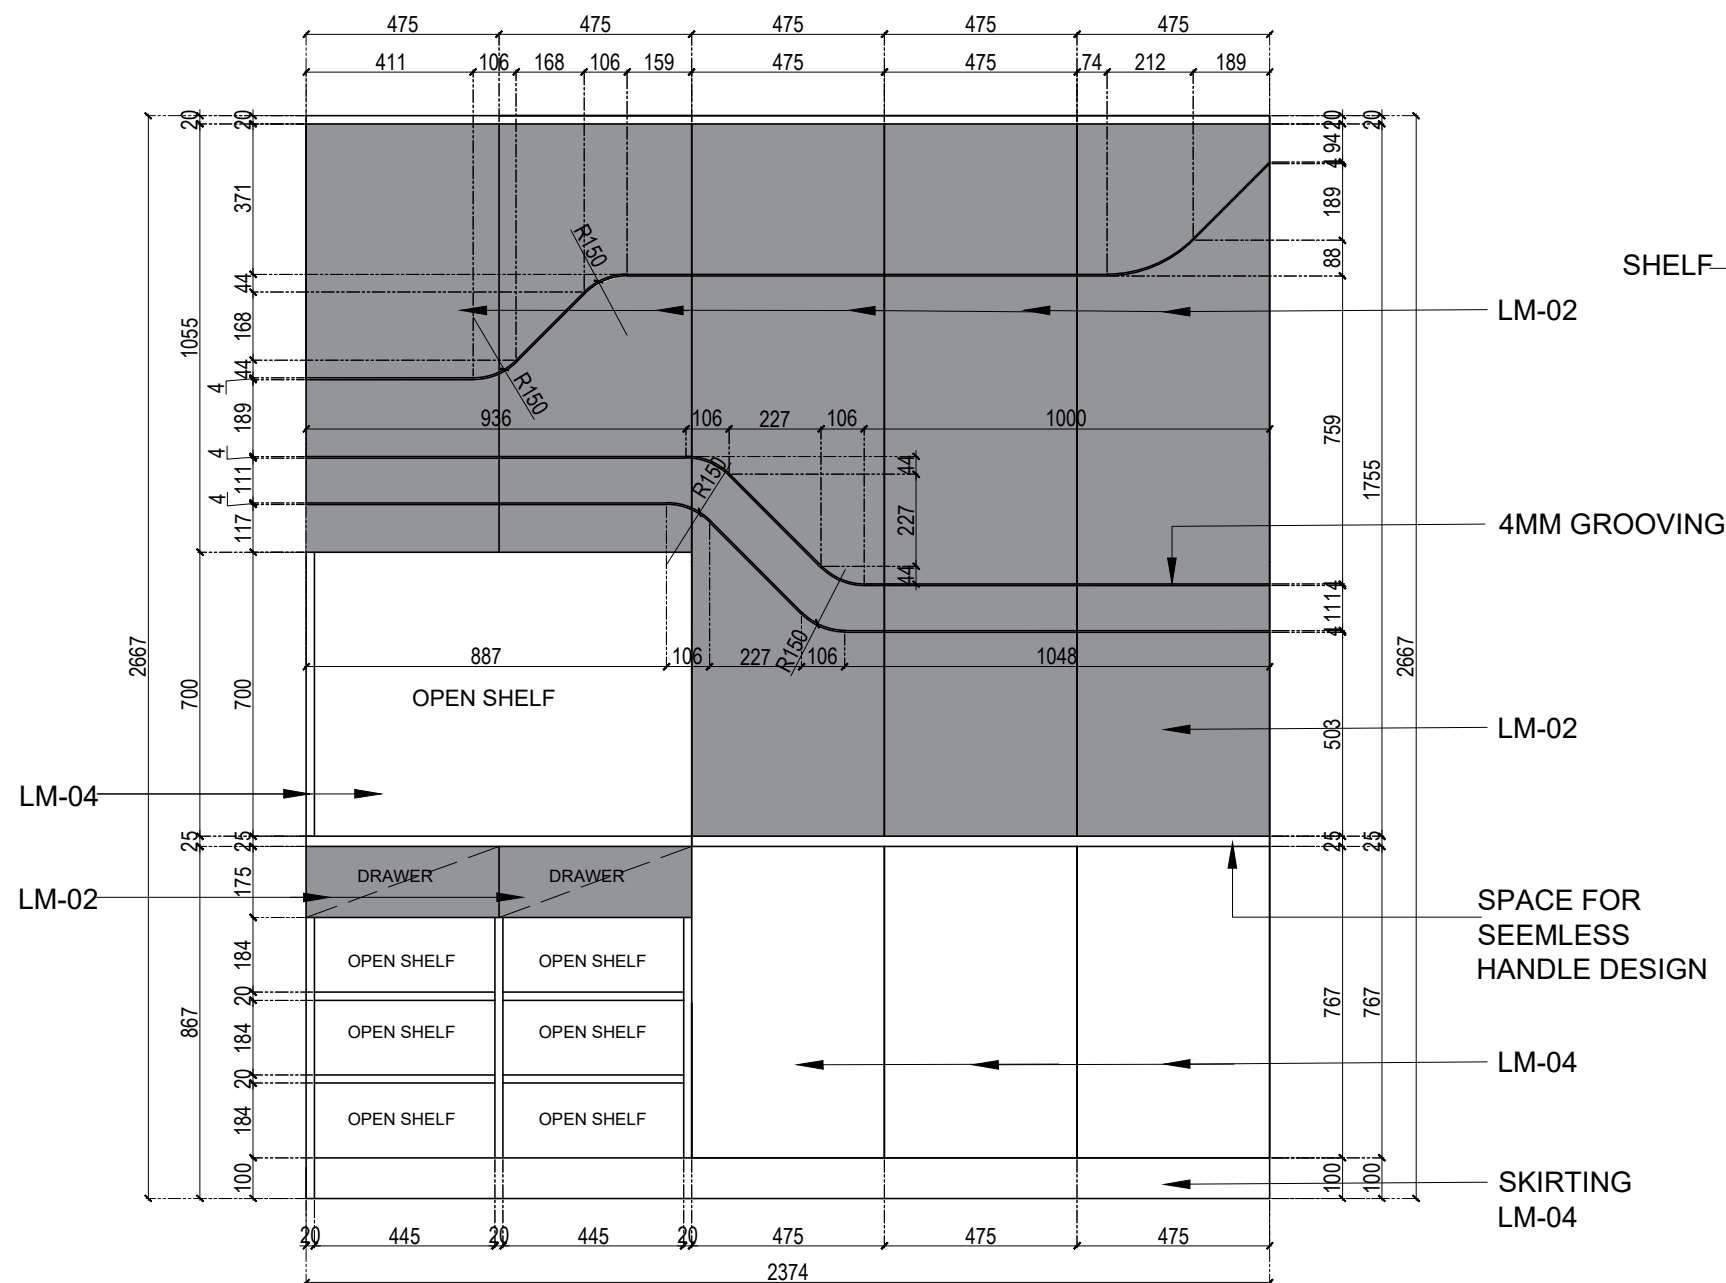



2 FRONT ELEVATION
WORKSTATION AREA

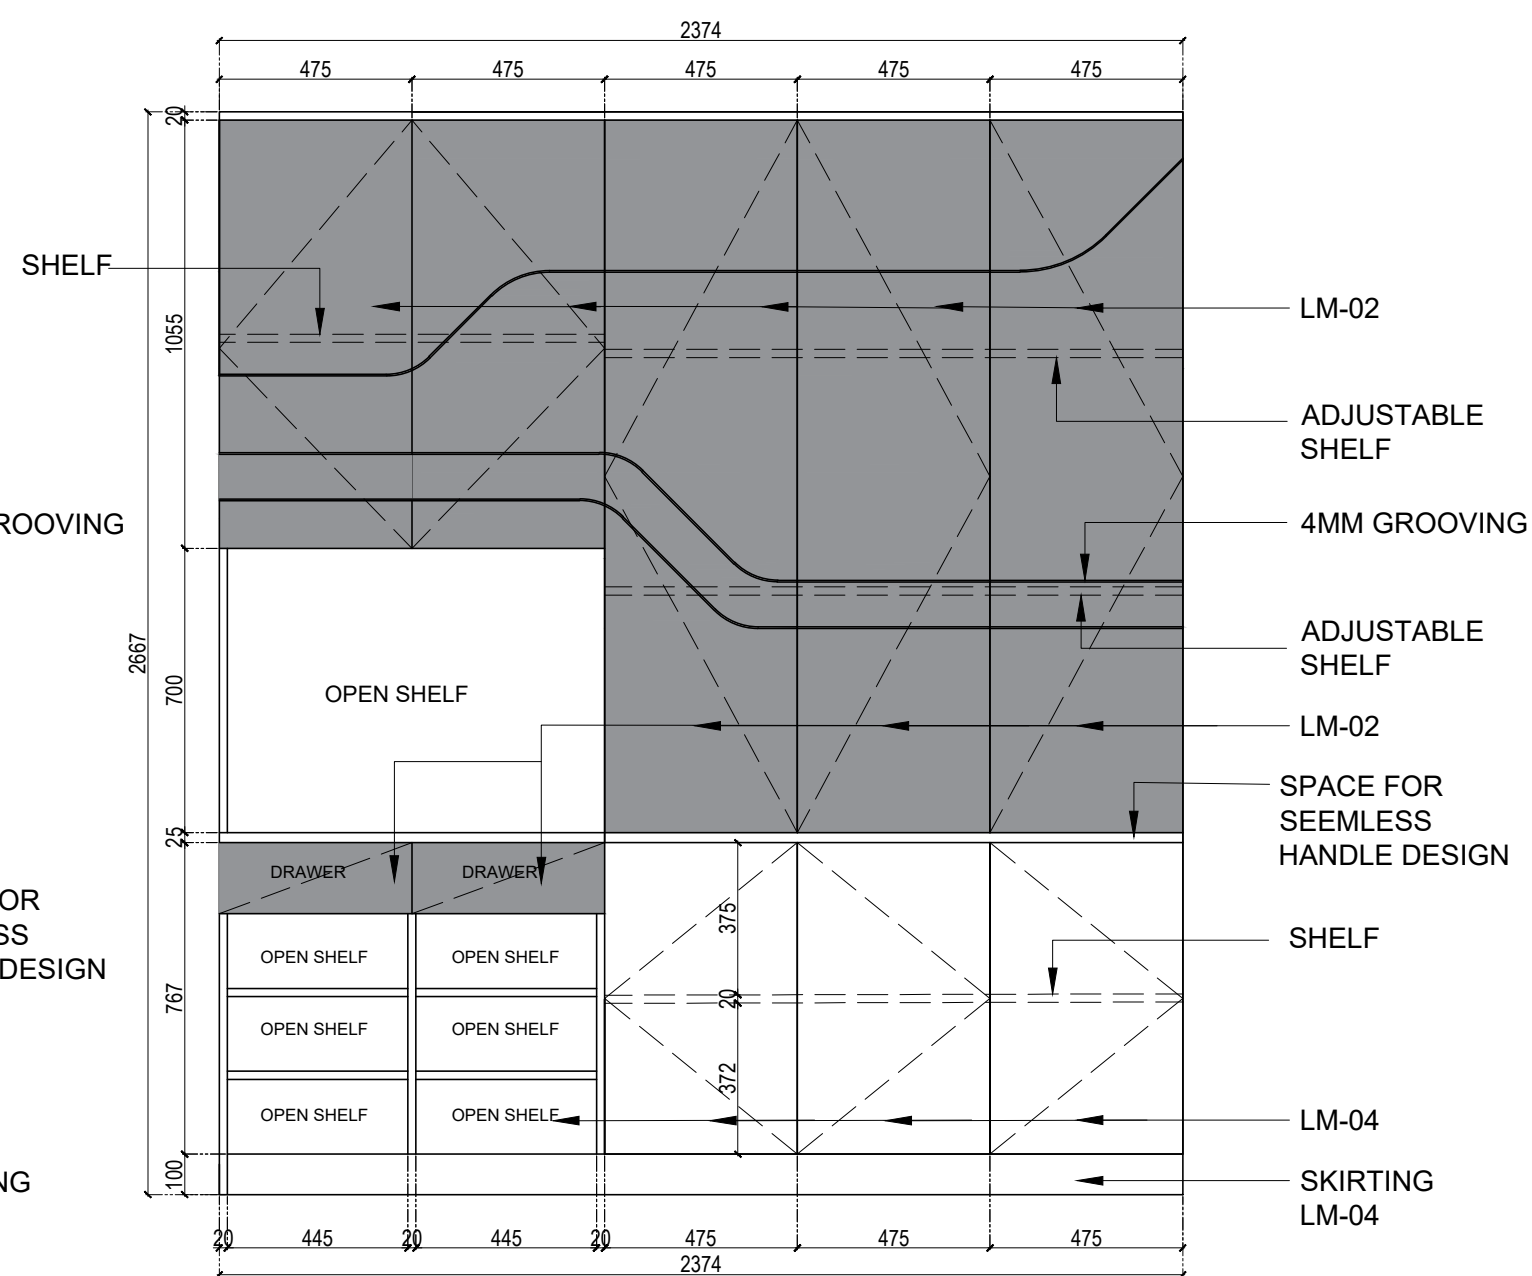


2.1 FRONT ELEVATION
WORKSTATION AREA

WORKSTATION AREA STORAGE

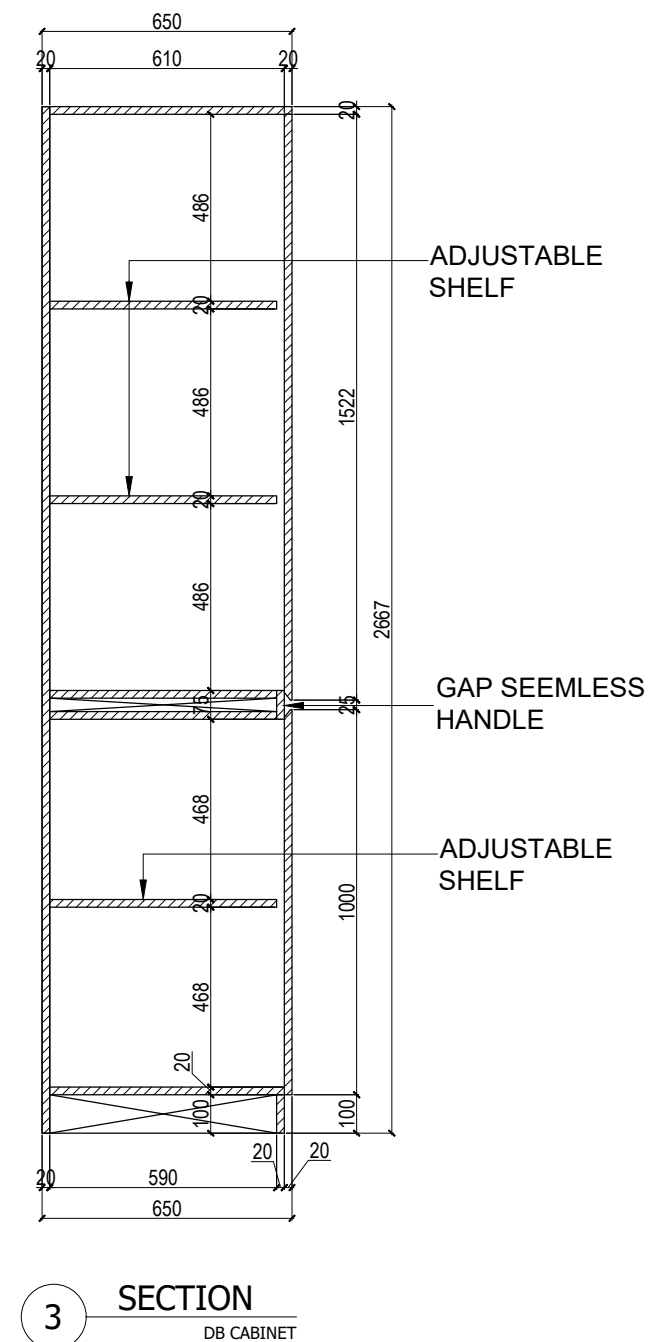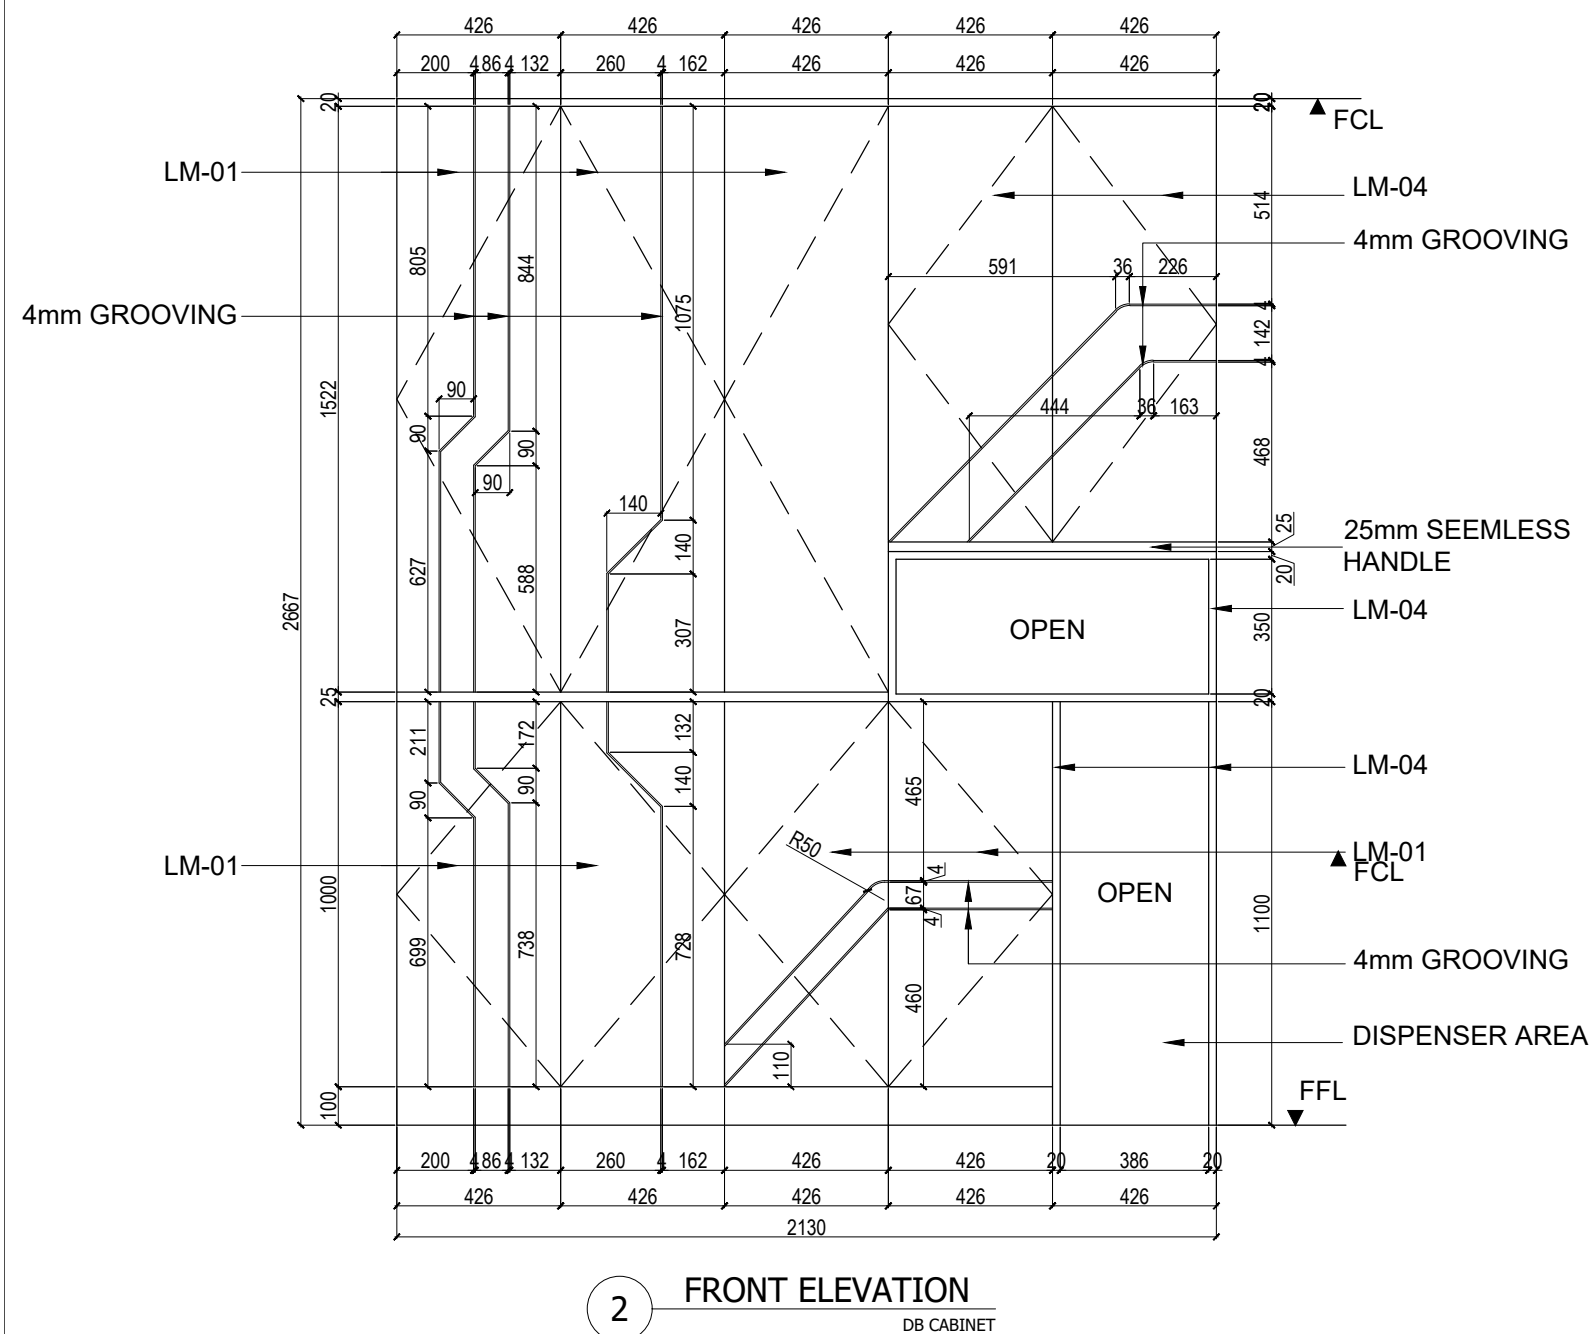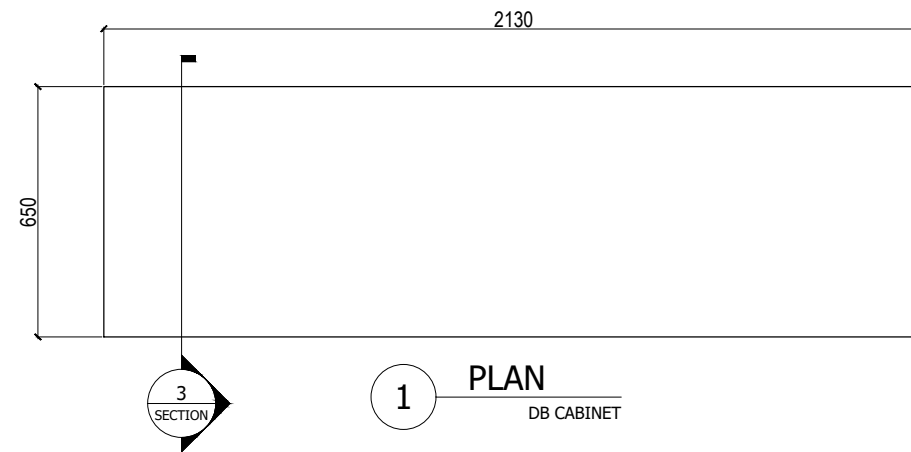
DB CABINET

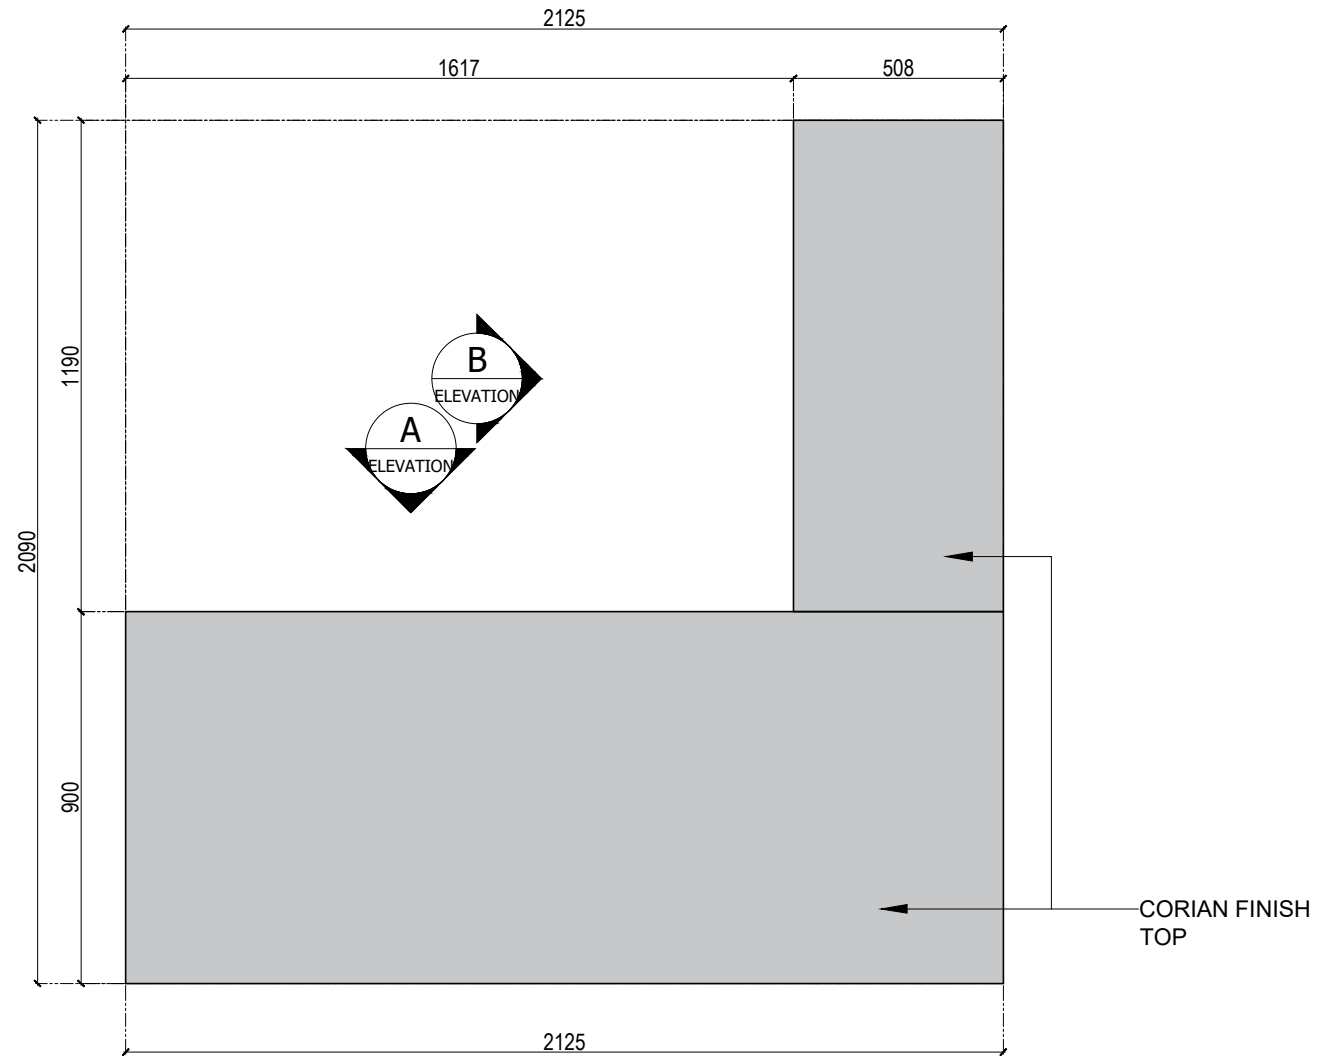


1 PLAN
MD WORKING TABLE

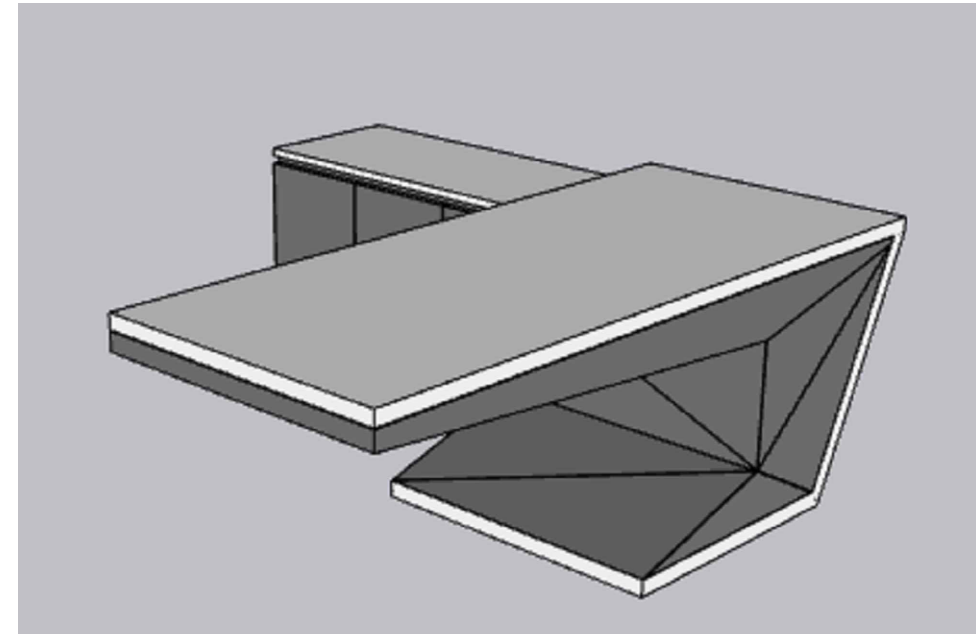

4 REFERENCE IMAGE
MD WORKING TABLE

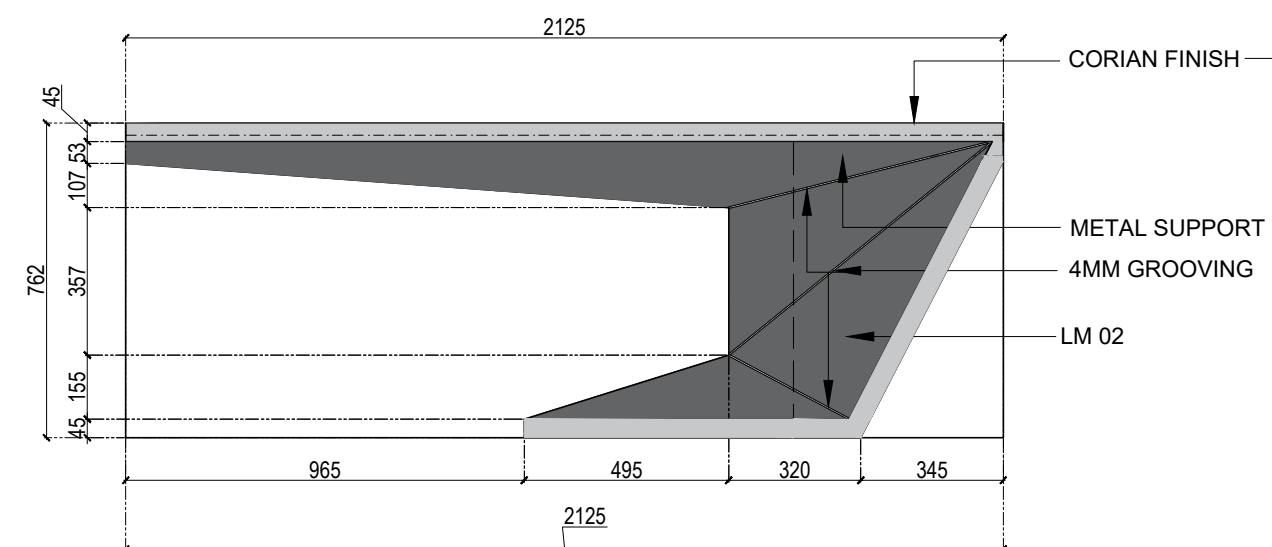


2 ELEVATION AT A
MD WORKING TABLE

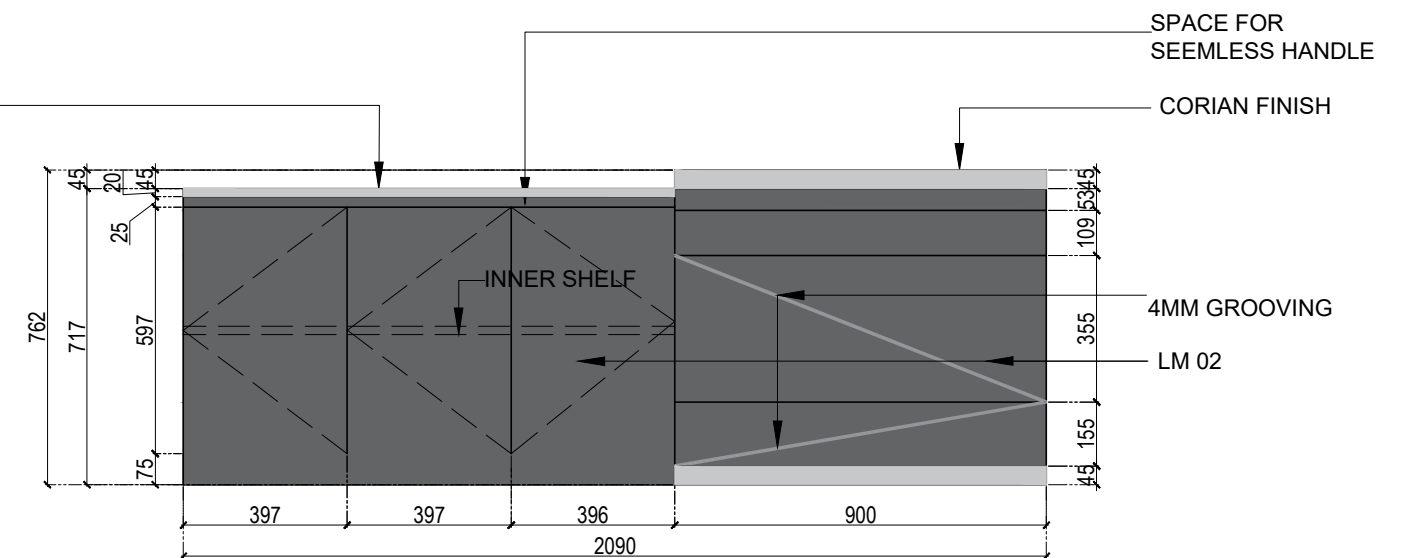


3 ELEVATION AT B
MD WORKING TABLE


MD WORKING TABLE

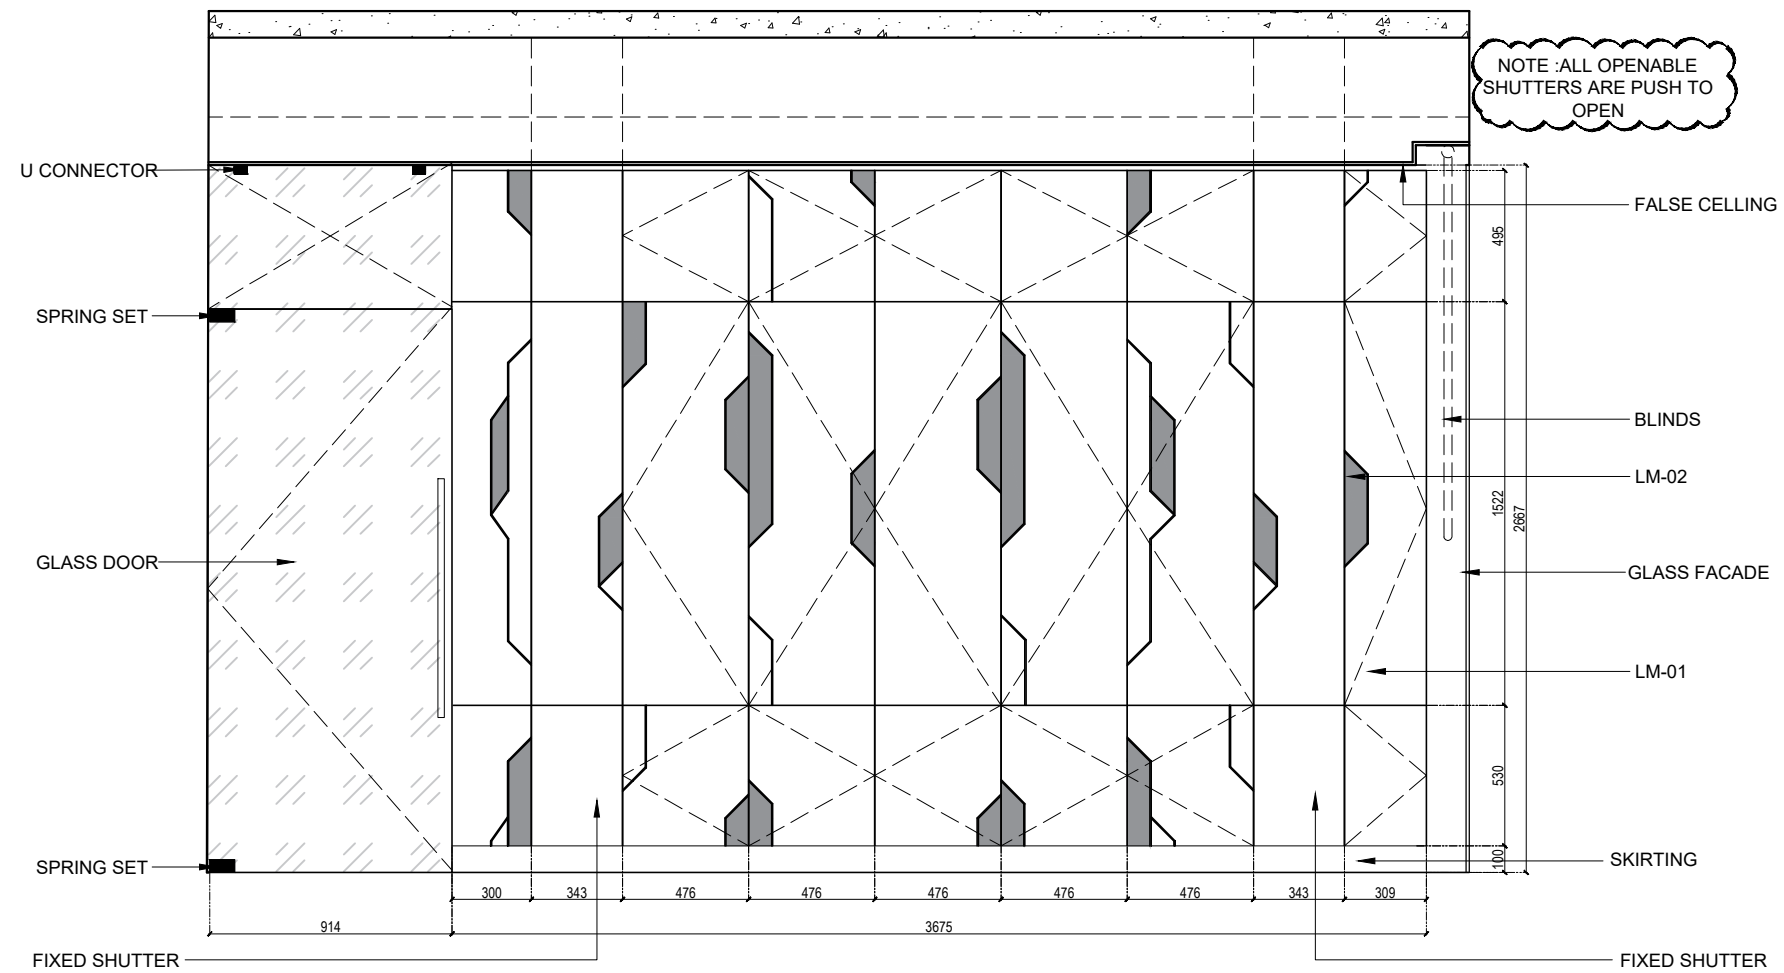


2.1 FRONT ELEVATION
MD STORAGE CABINETE

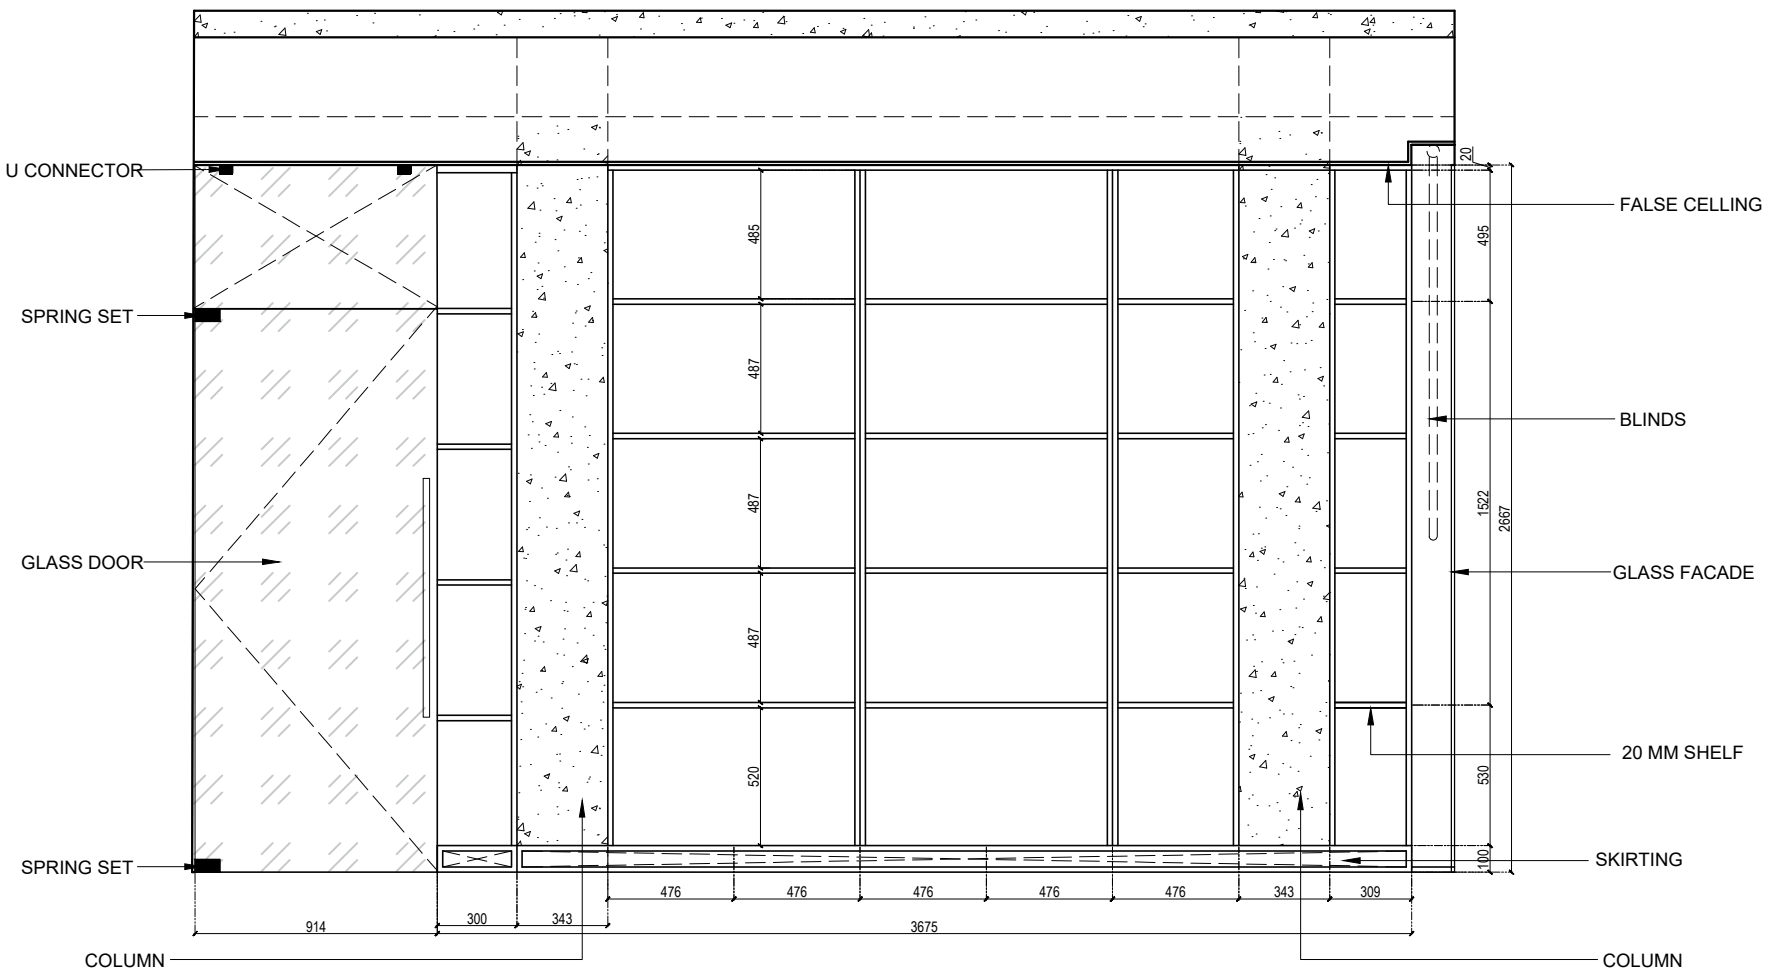


4 INNER ELEVATION
MD STORAGE CABINETE

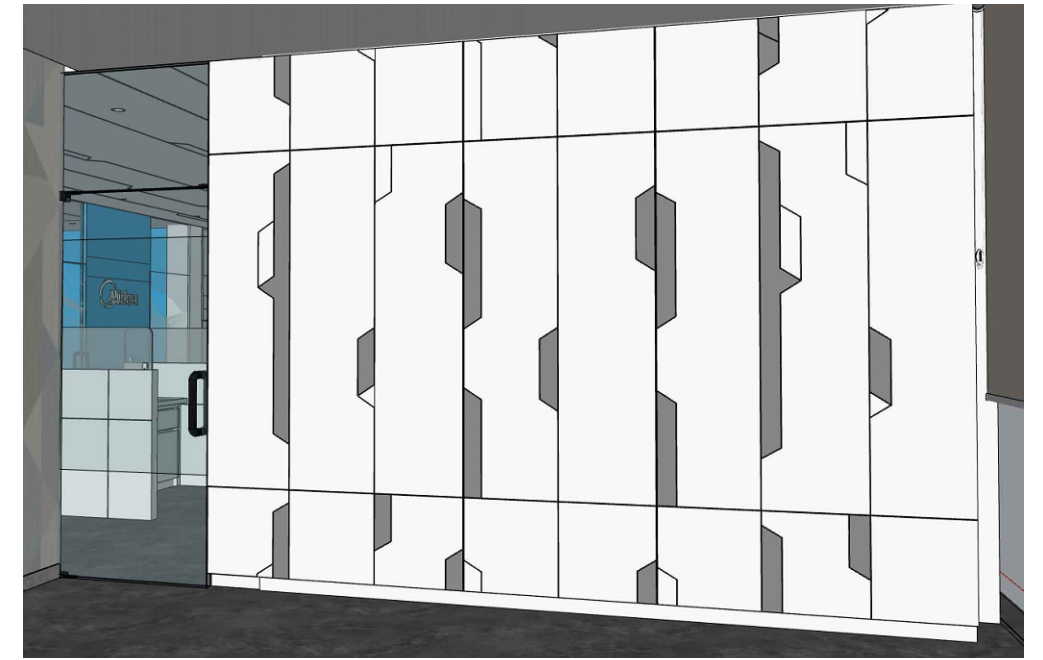


5 REFERENCE IMAGE
MD STORAGE CABINETE

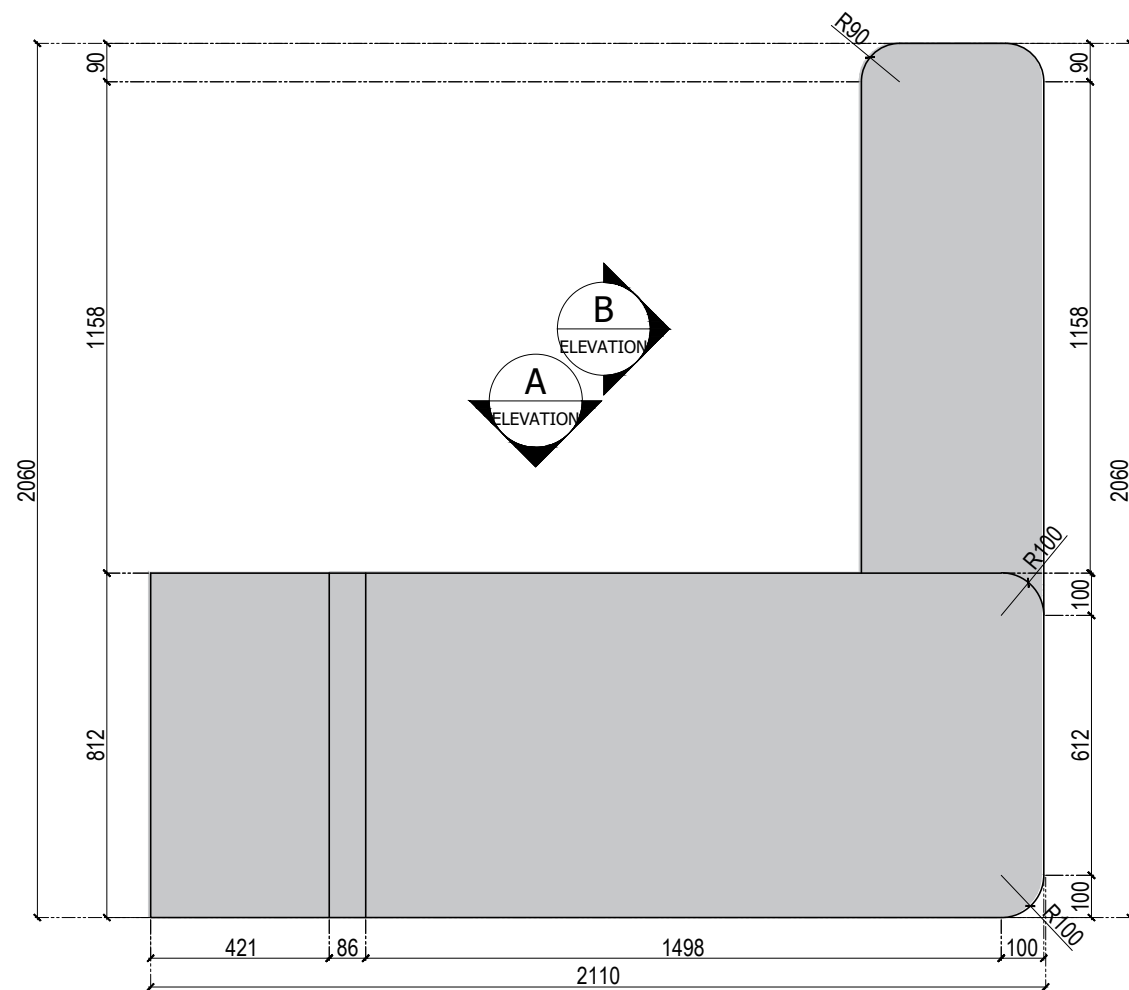


1 PLAN
DIRECTOR ROOM

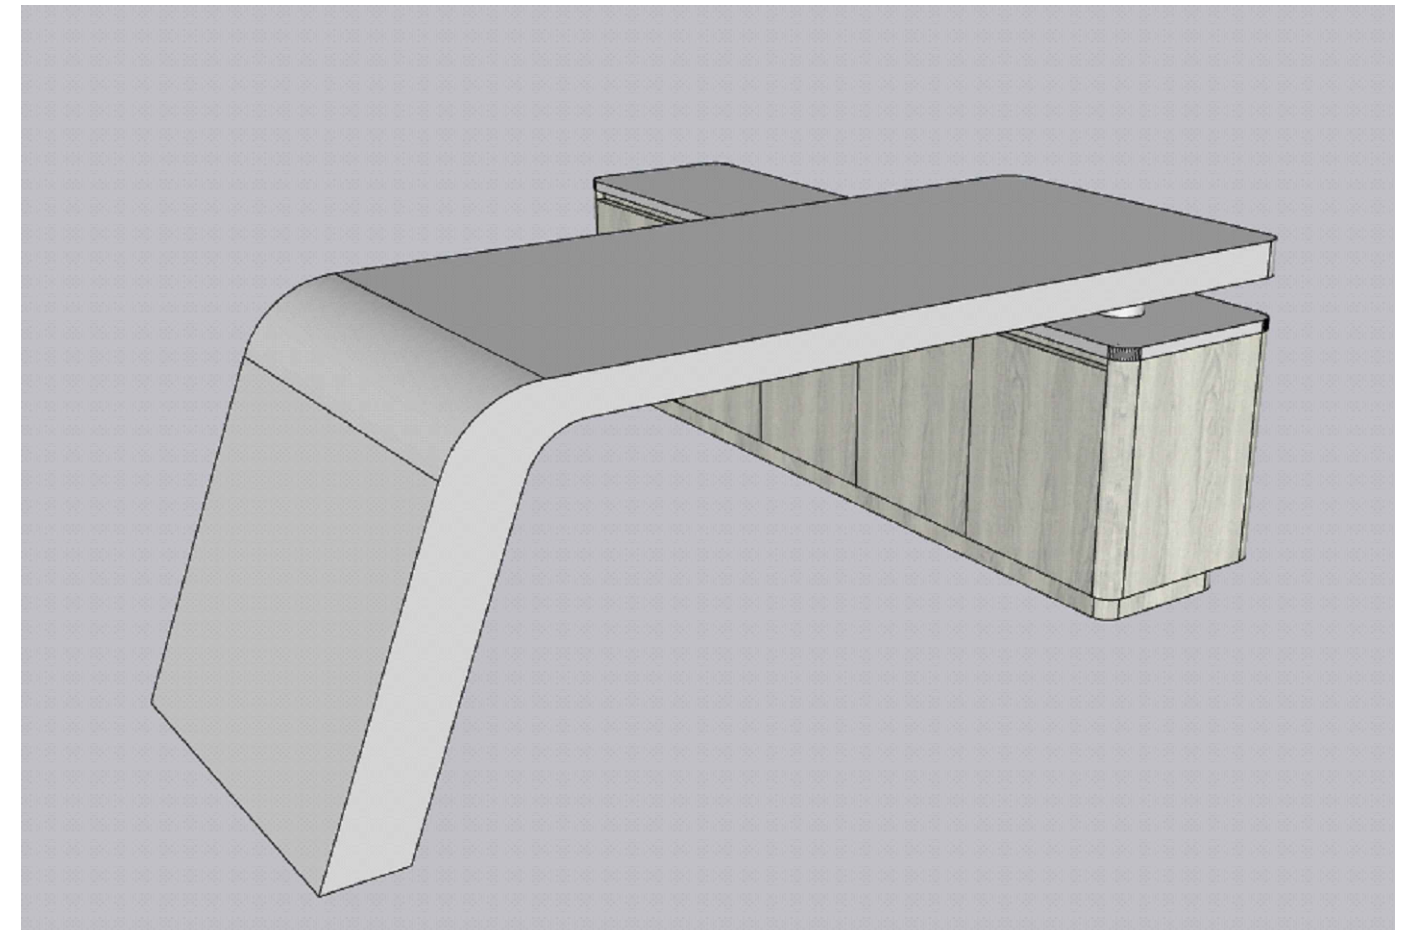

4 REFERENCE IMAGE
DIRECTOR ROOM



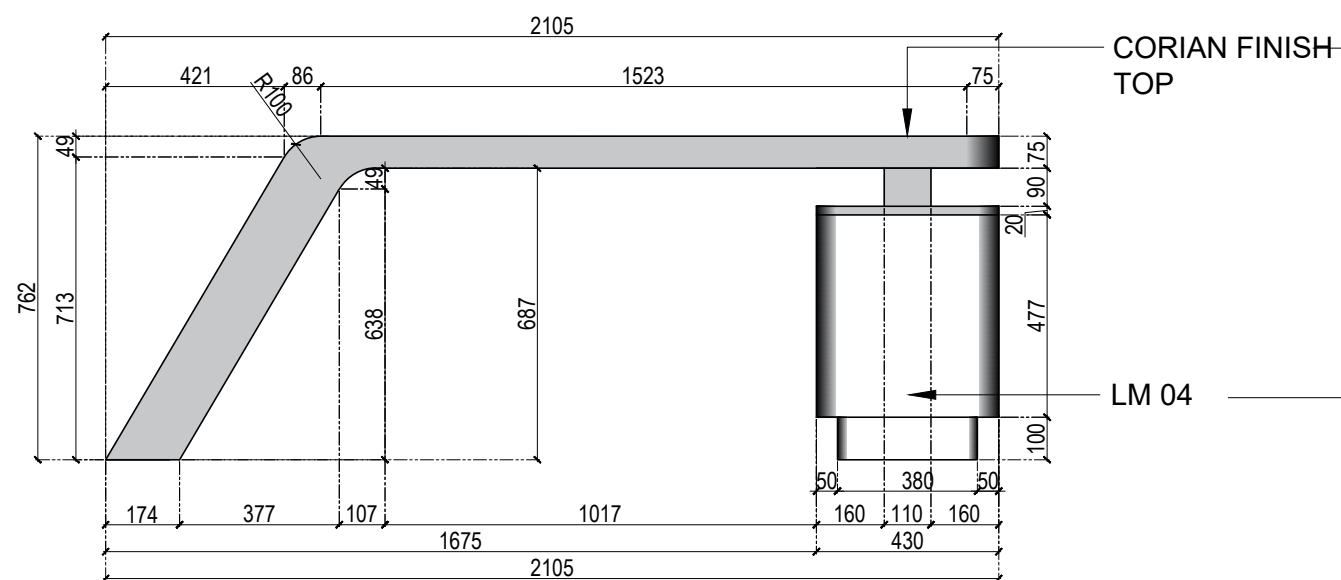



2 ELEVATION AT A
DIRECTOR ROOM

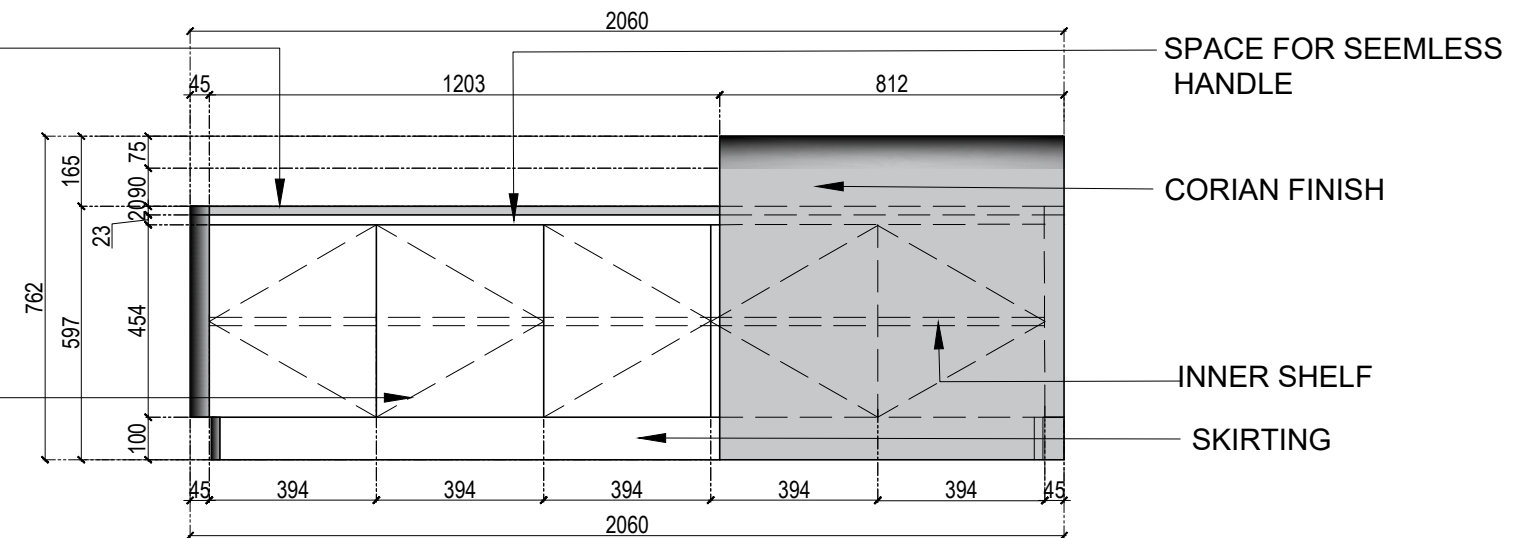


3 ELEVATION AT B
DIRECTOR ROOM

DIRECTOR WORKING TABLE

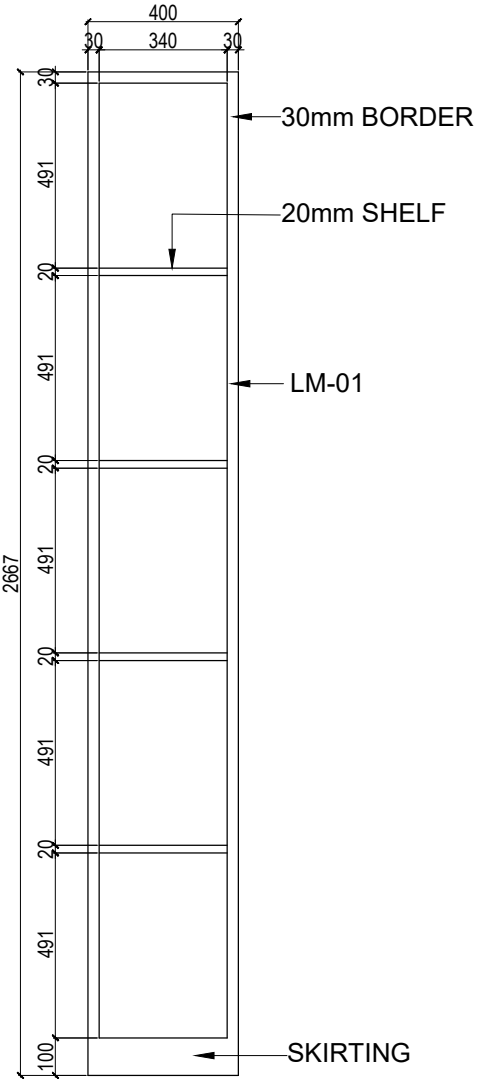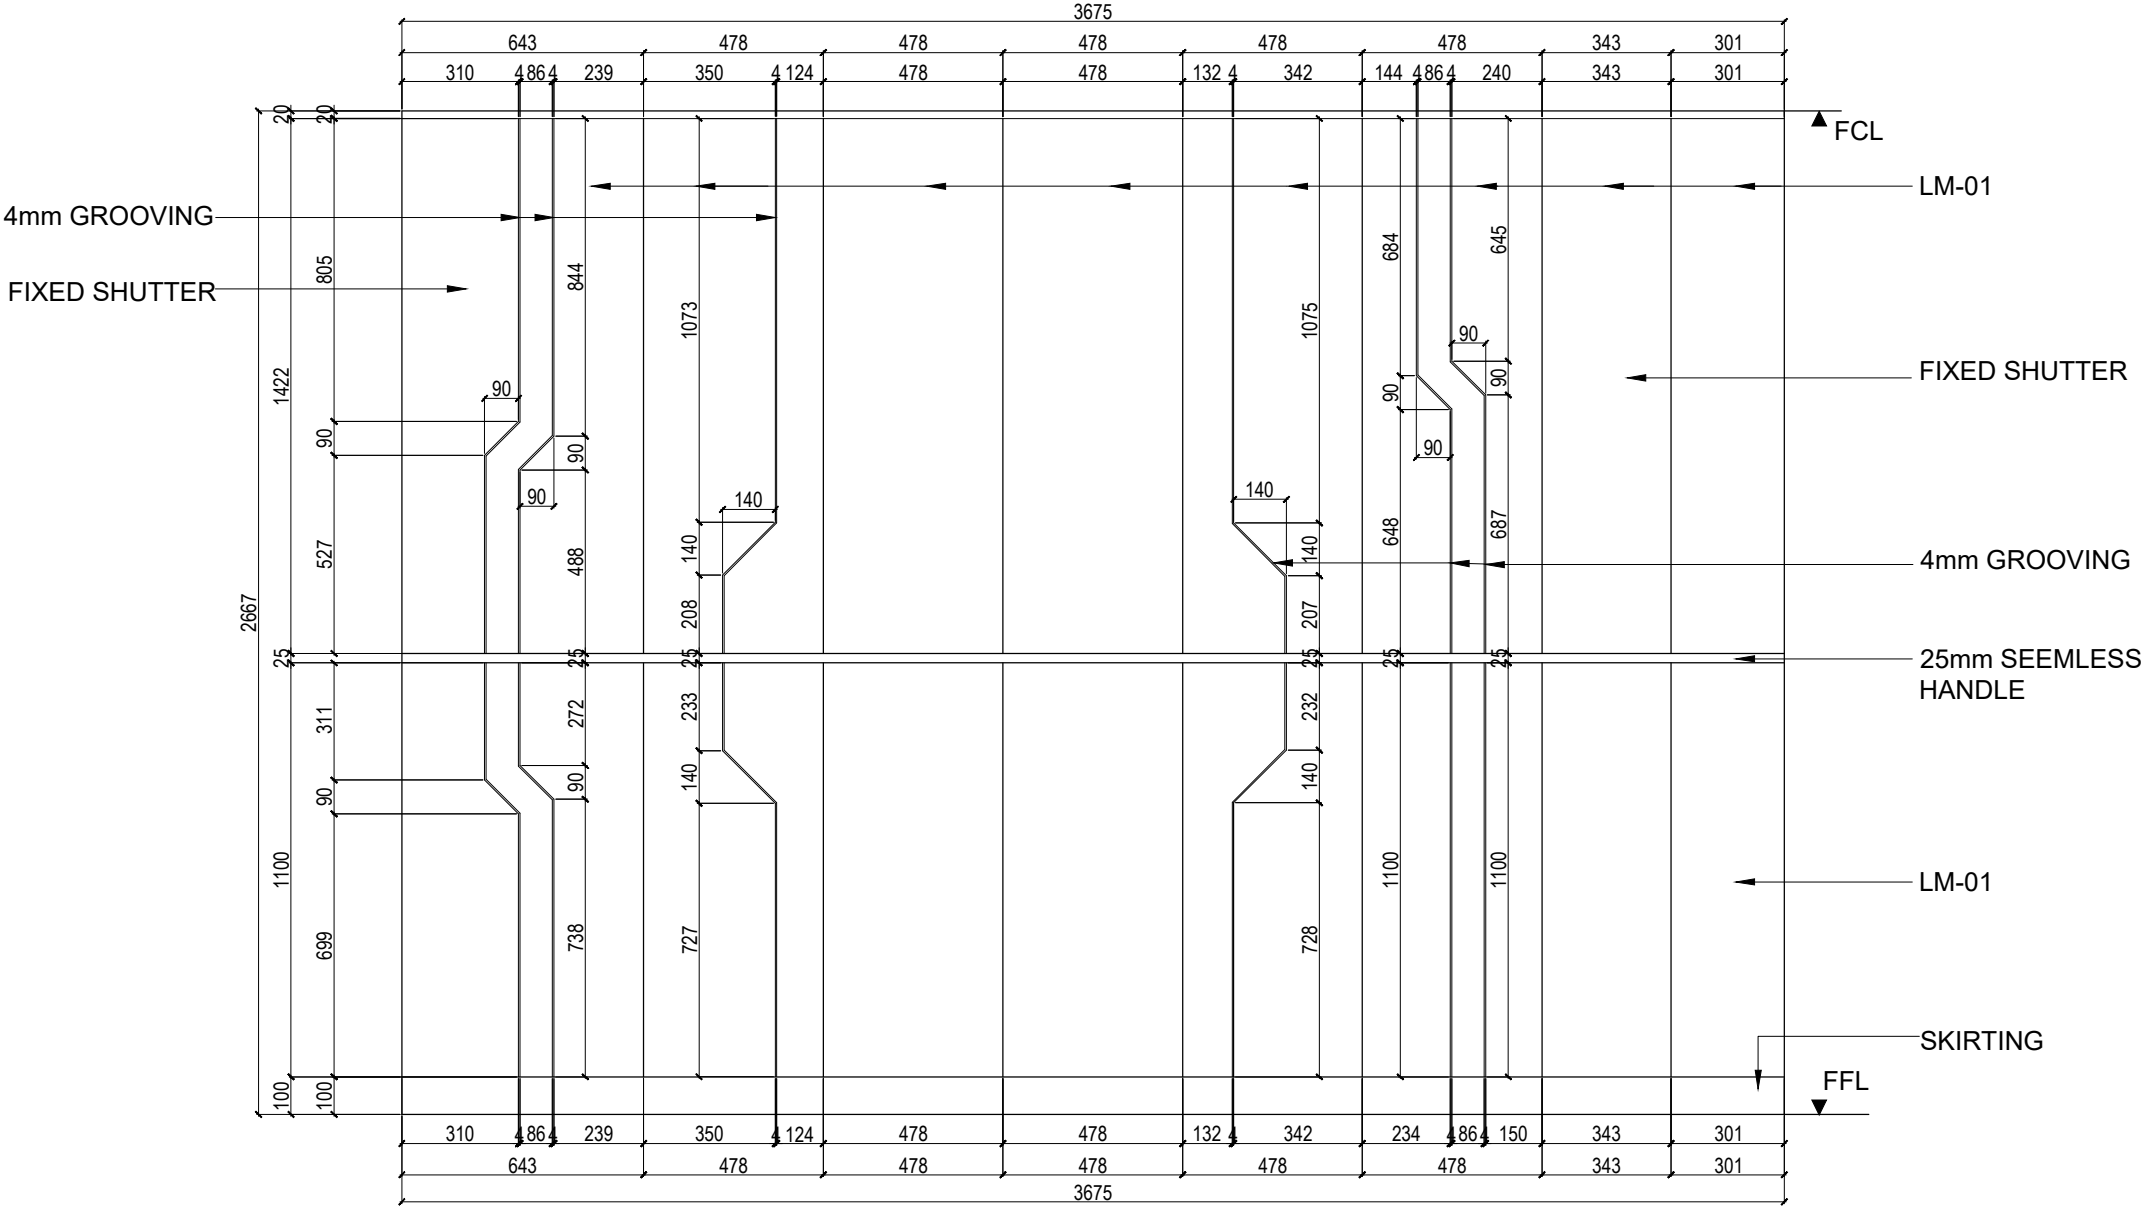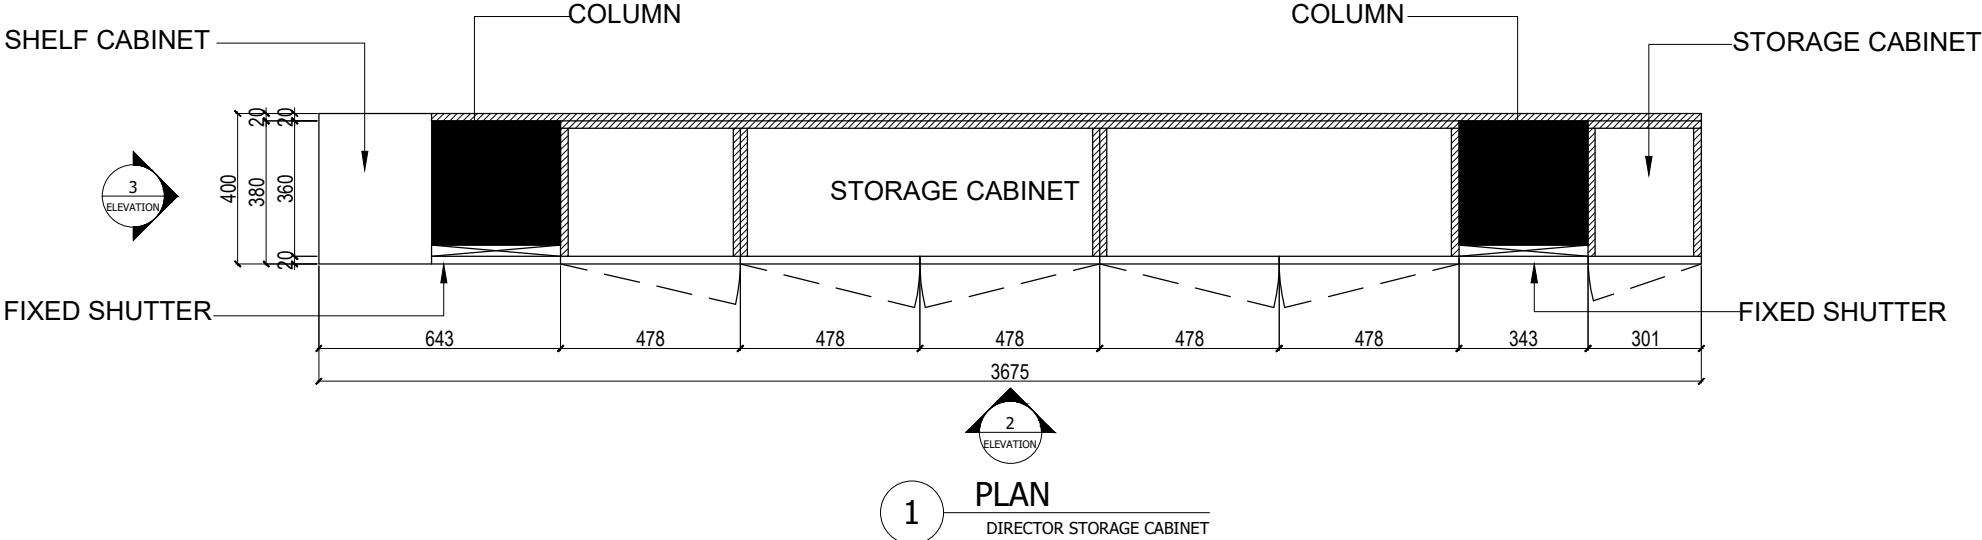


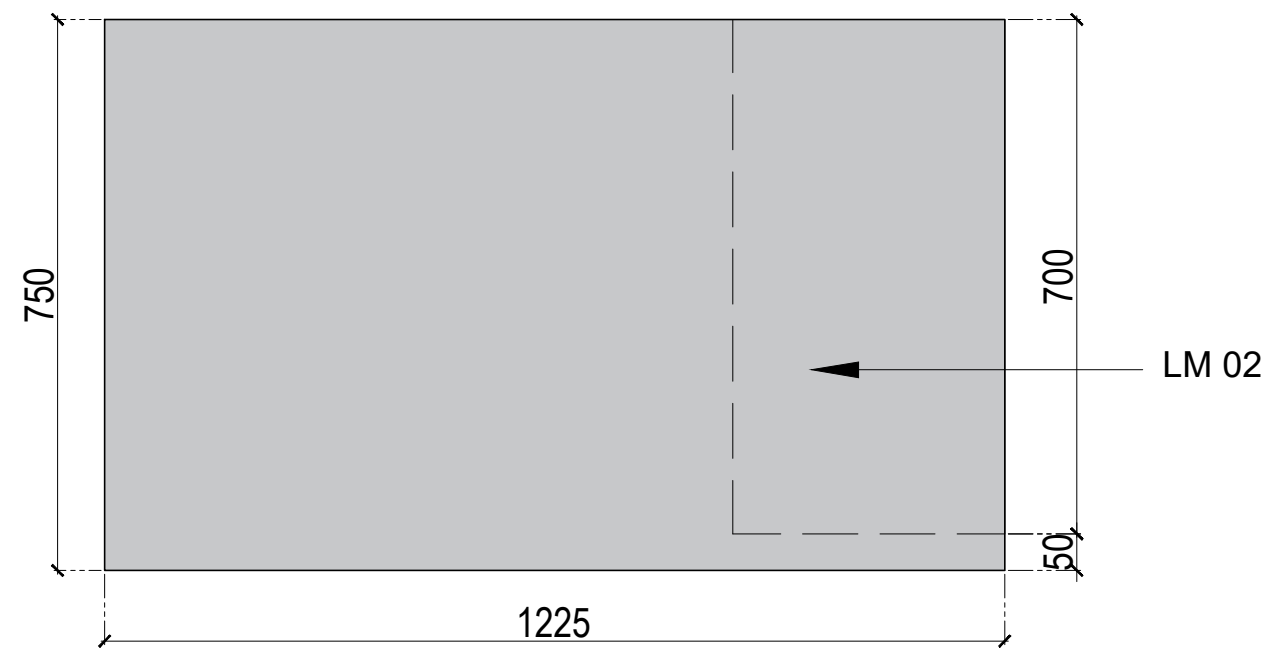


1 PLAN
WORK STATION

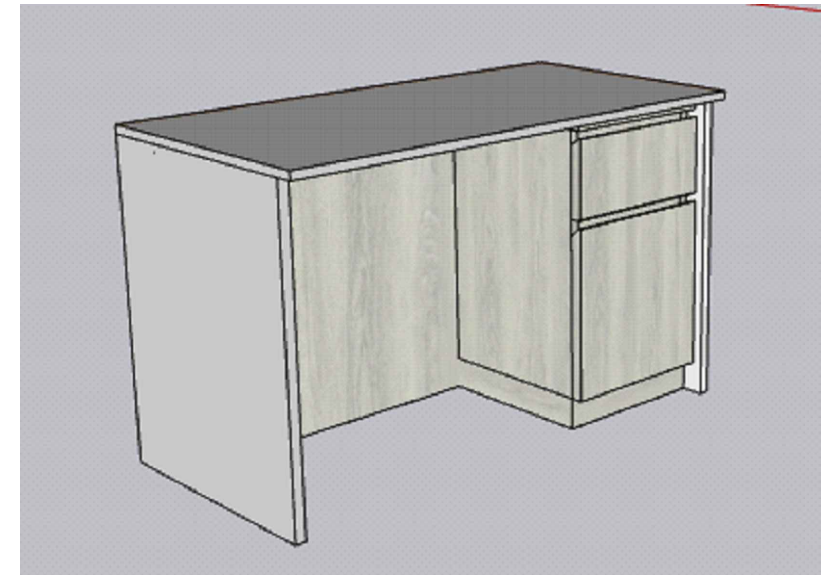

4 REFERENCE IMAGE
WORK STATION

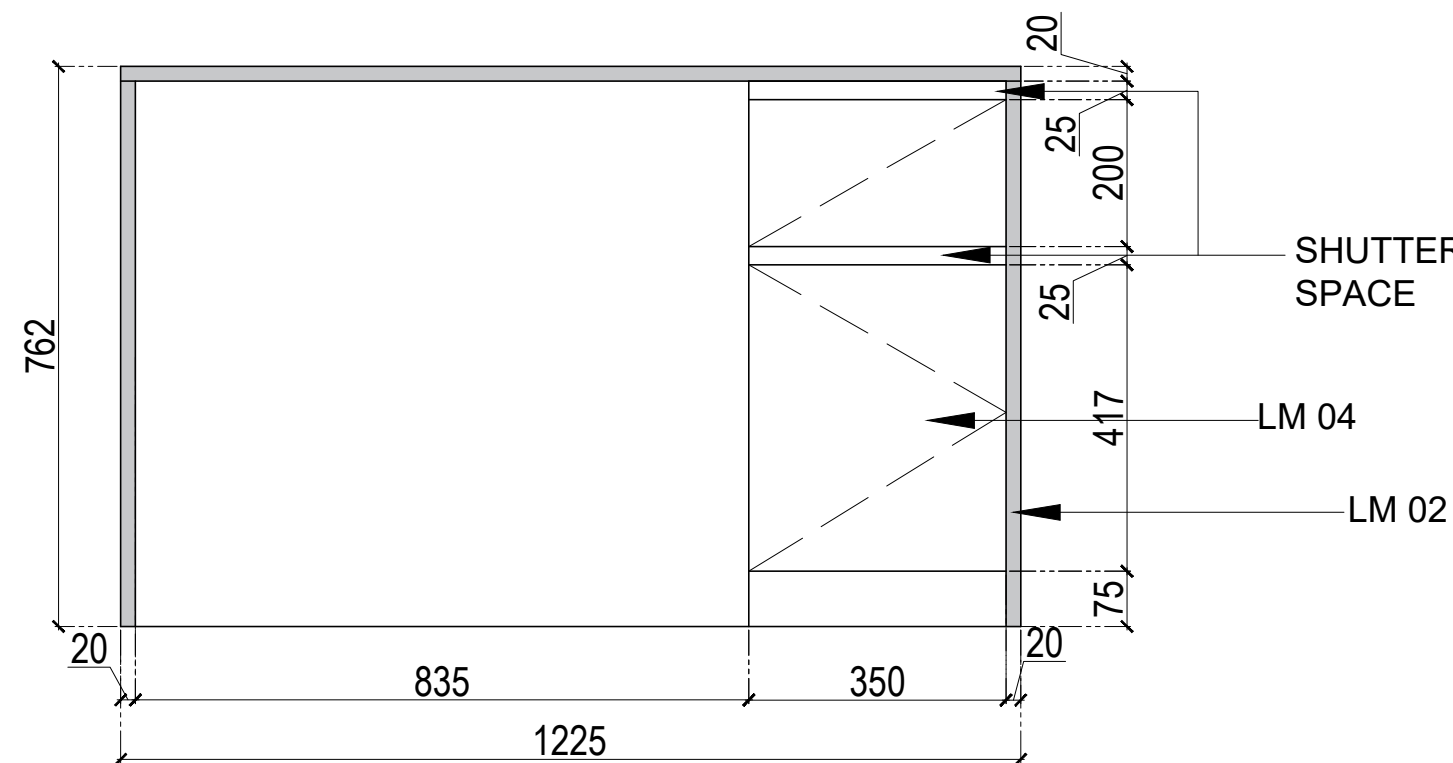


2 FRONT ELEVATION
WORK STATION

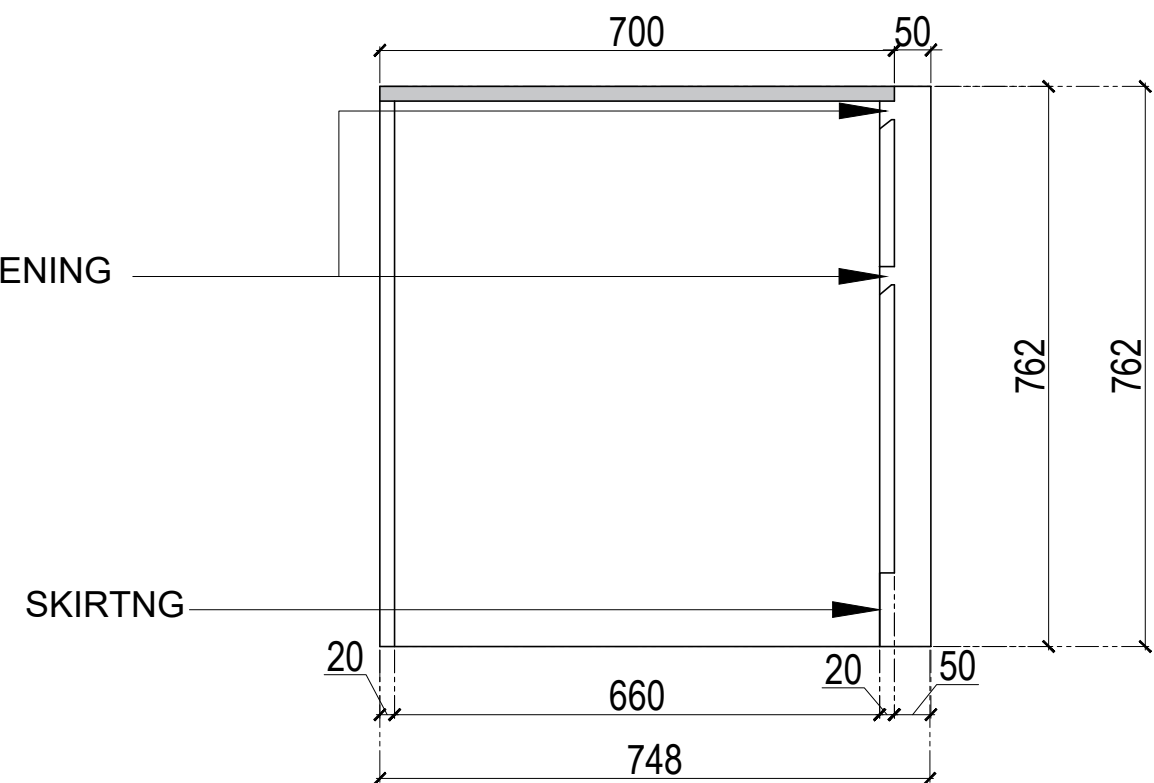


3 SIDE ELEVATION
WORK STATION


WORK STATION AREA WORK STATION

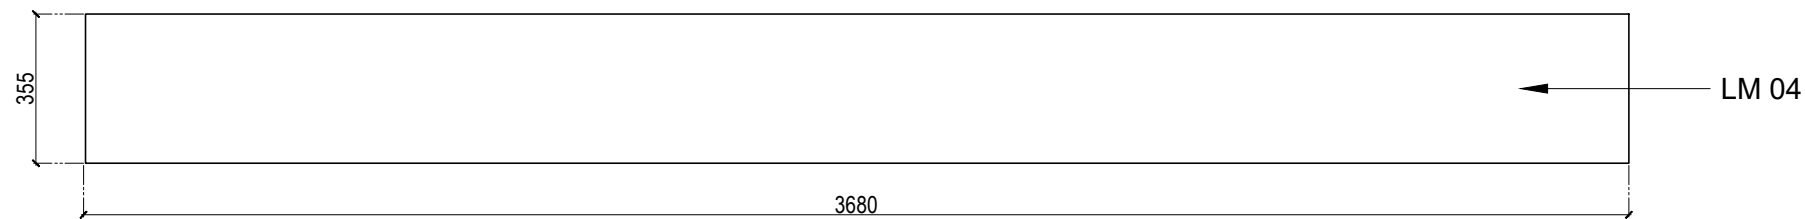

1 PLAN
UPPERHEAD CABINATE

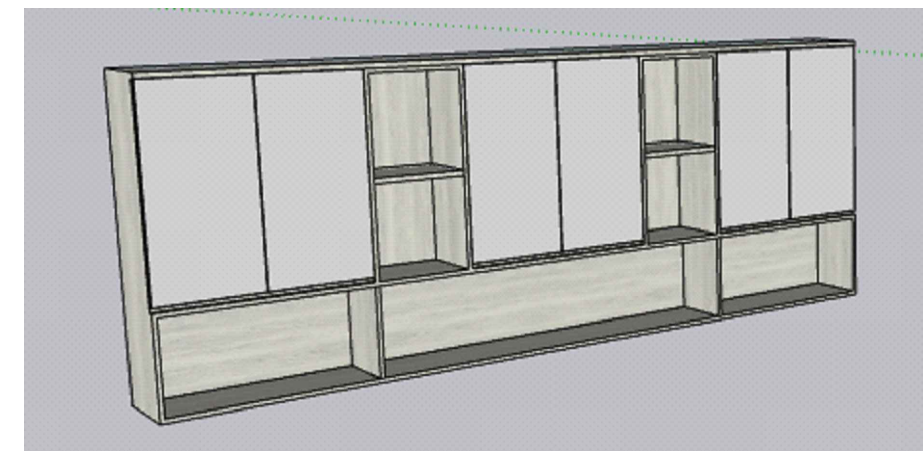


4 REFERENCE IMAGE
UPPERHEAD CABINATE

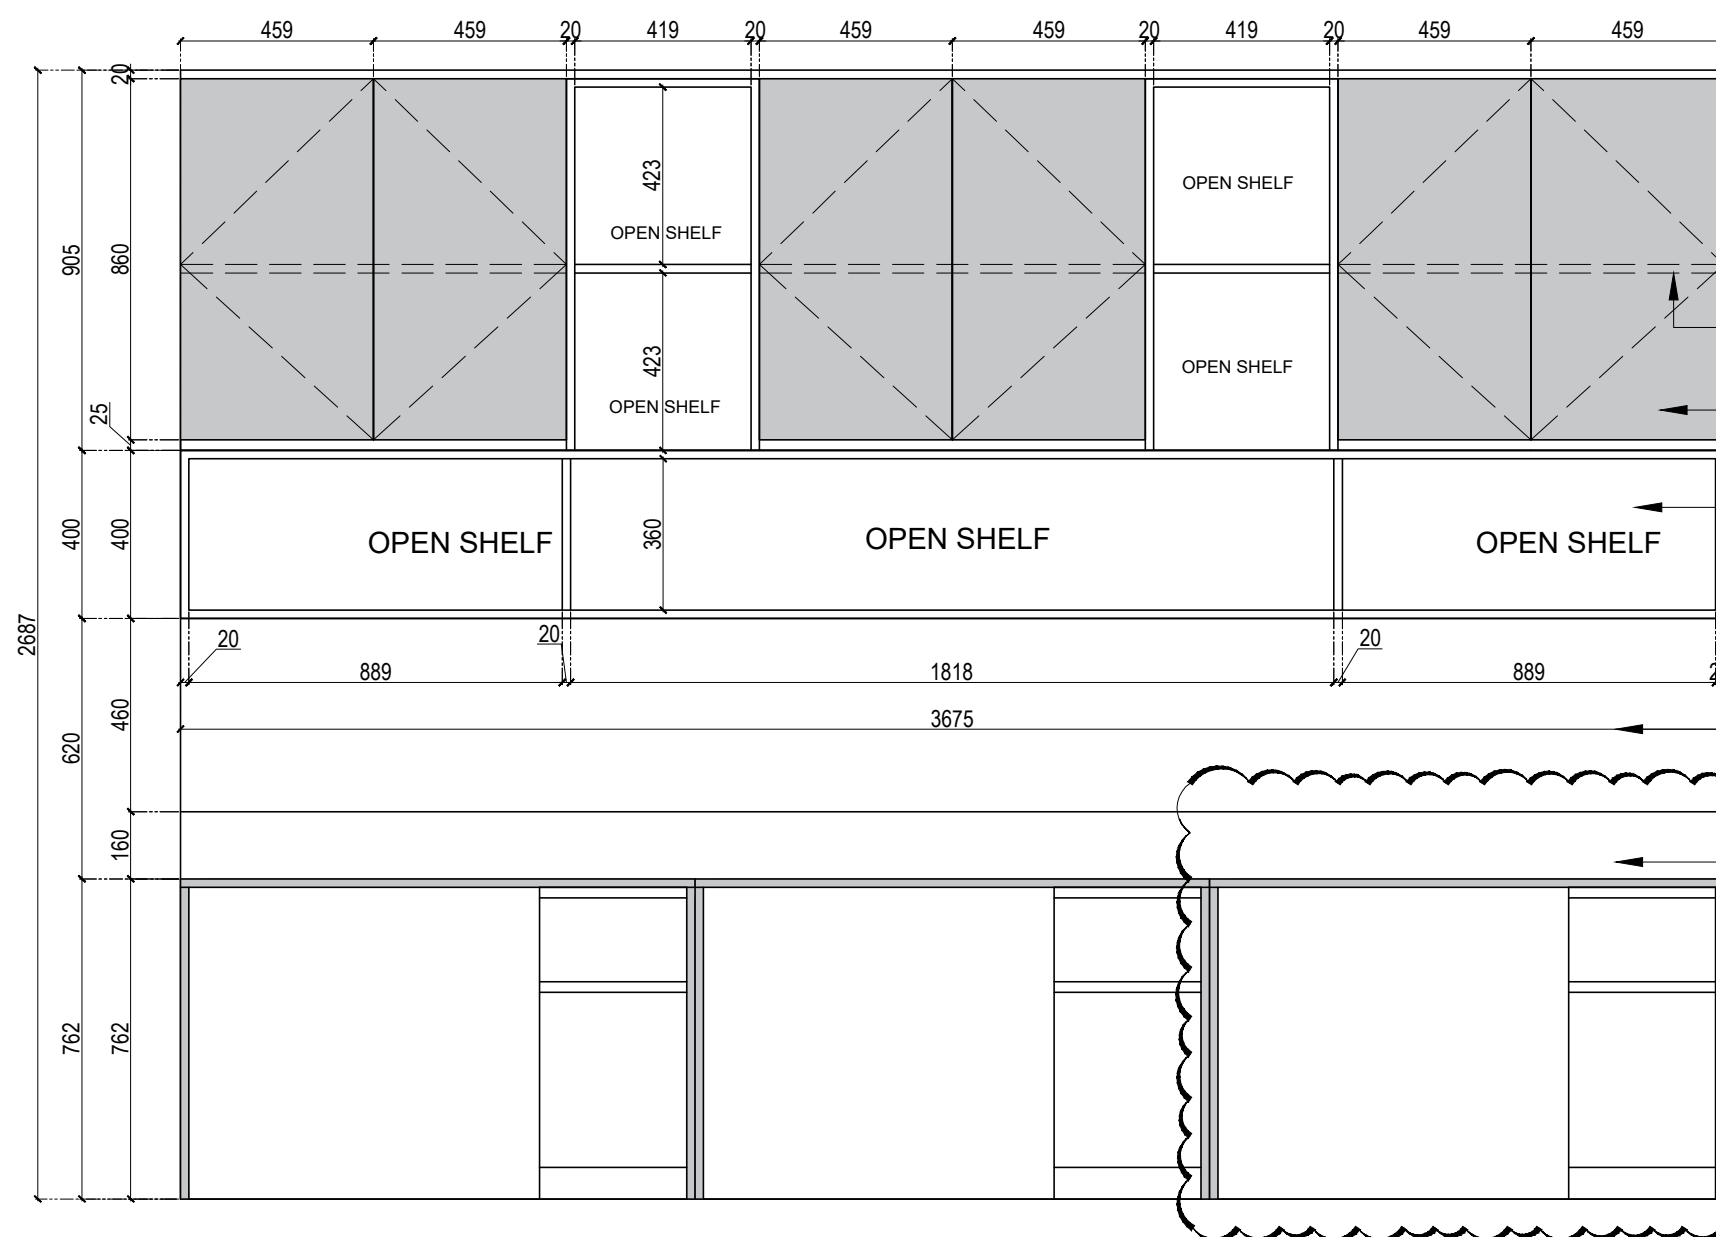



2 FRONT ELEVATION
UPPERHEAD CABINATE

INNER SHELF OF 20 MM
LM 02
LM 04
SPACE FOR OPENING SHUTTER
LAMINATE FINISH/BULLETIN BOARD AS REQUIRMENT
LM 04

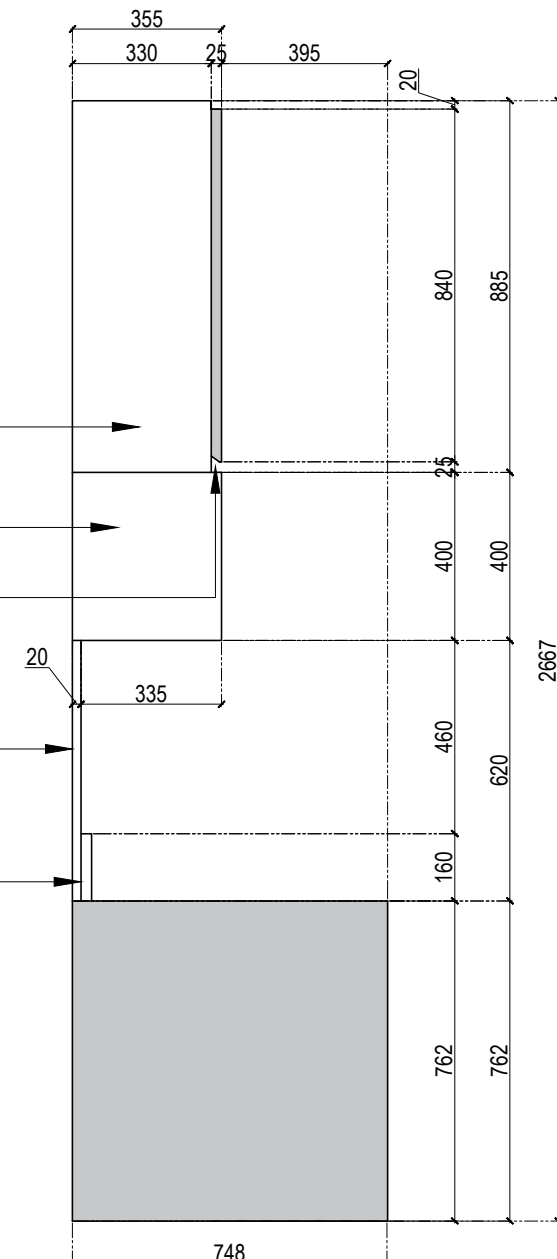


3 SIDE ELEVATION
UPPERHEAD CABINATE


WORK STATION AREA UPPER CABINATE

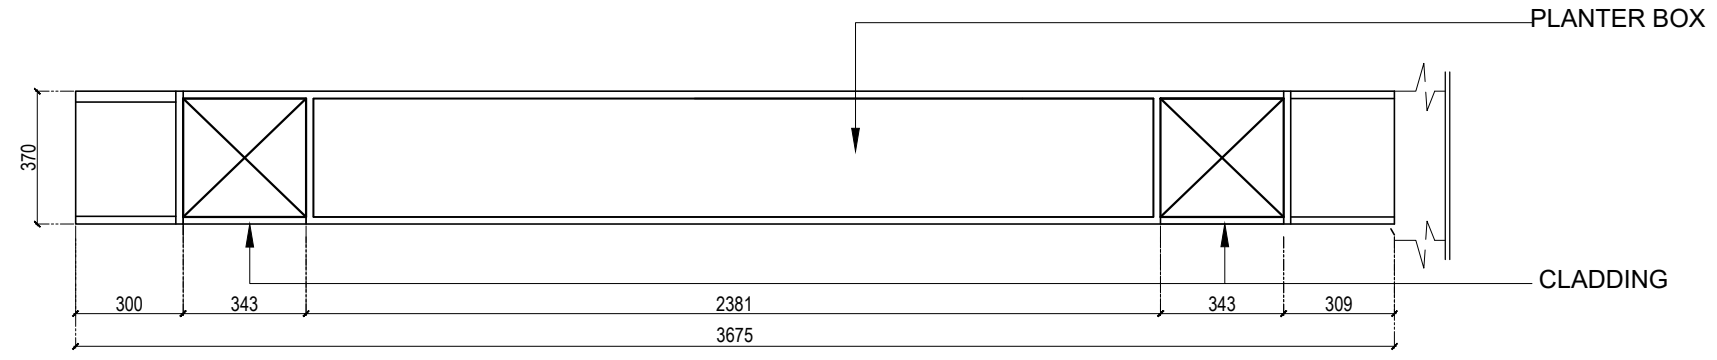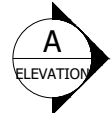

1 PLAN
WORKSTATION AREA PLANTER BOX

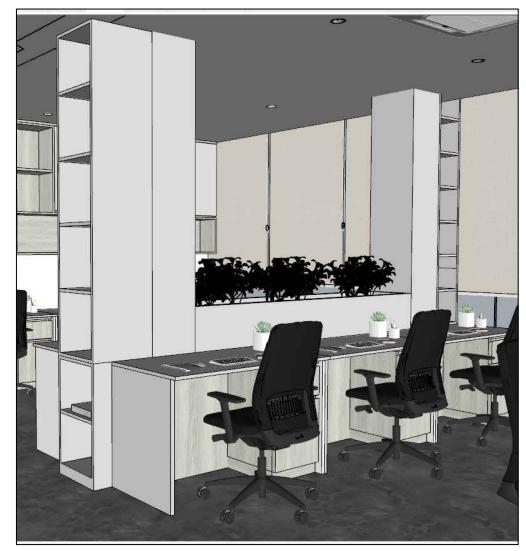

1 REFERENCE IMAGE
WORKSTATION AREA PLANTER BOX

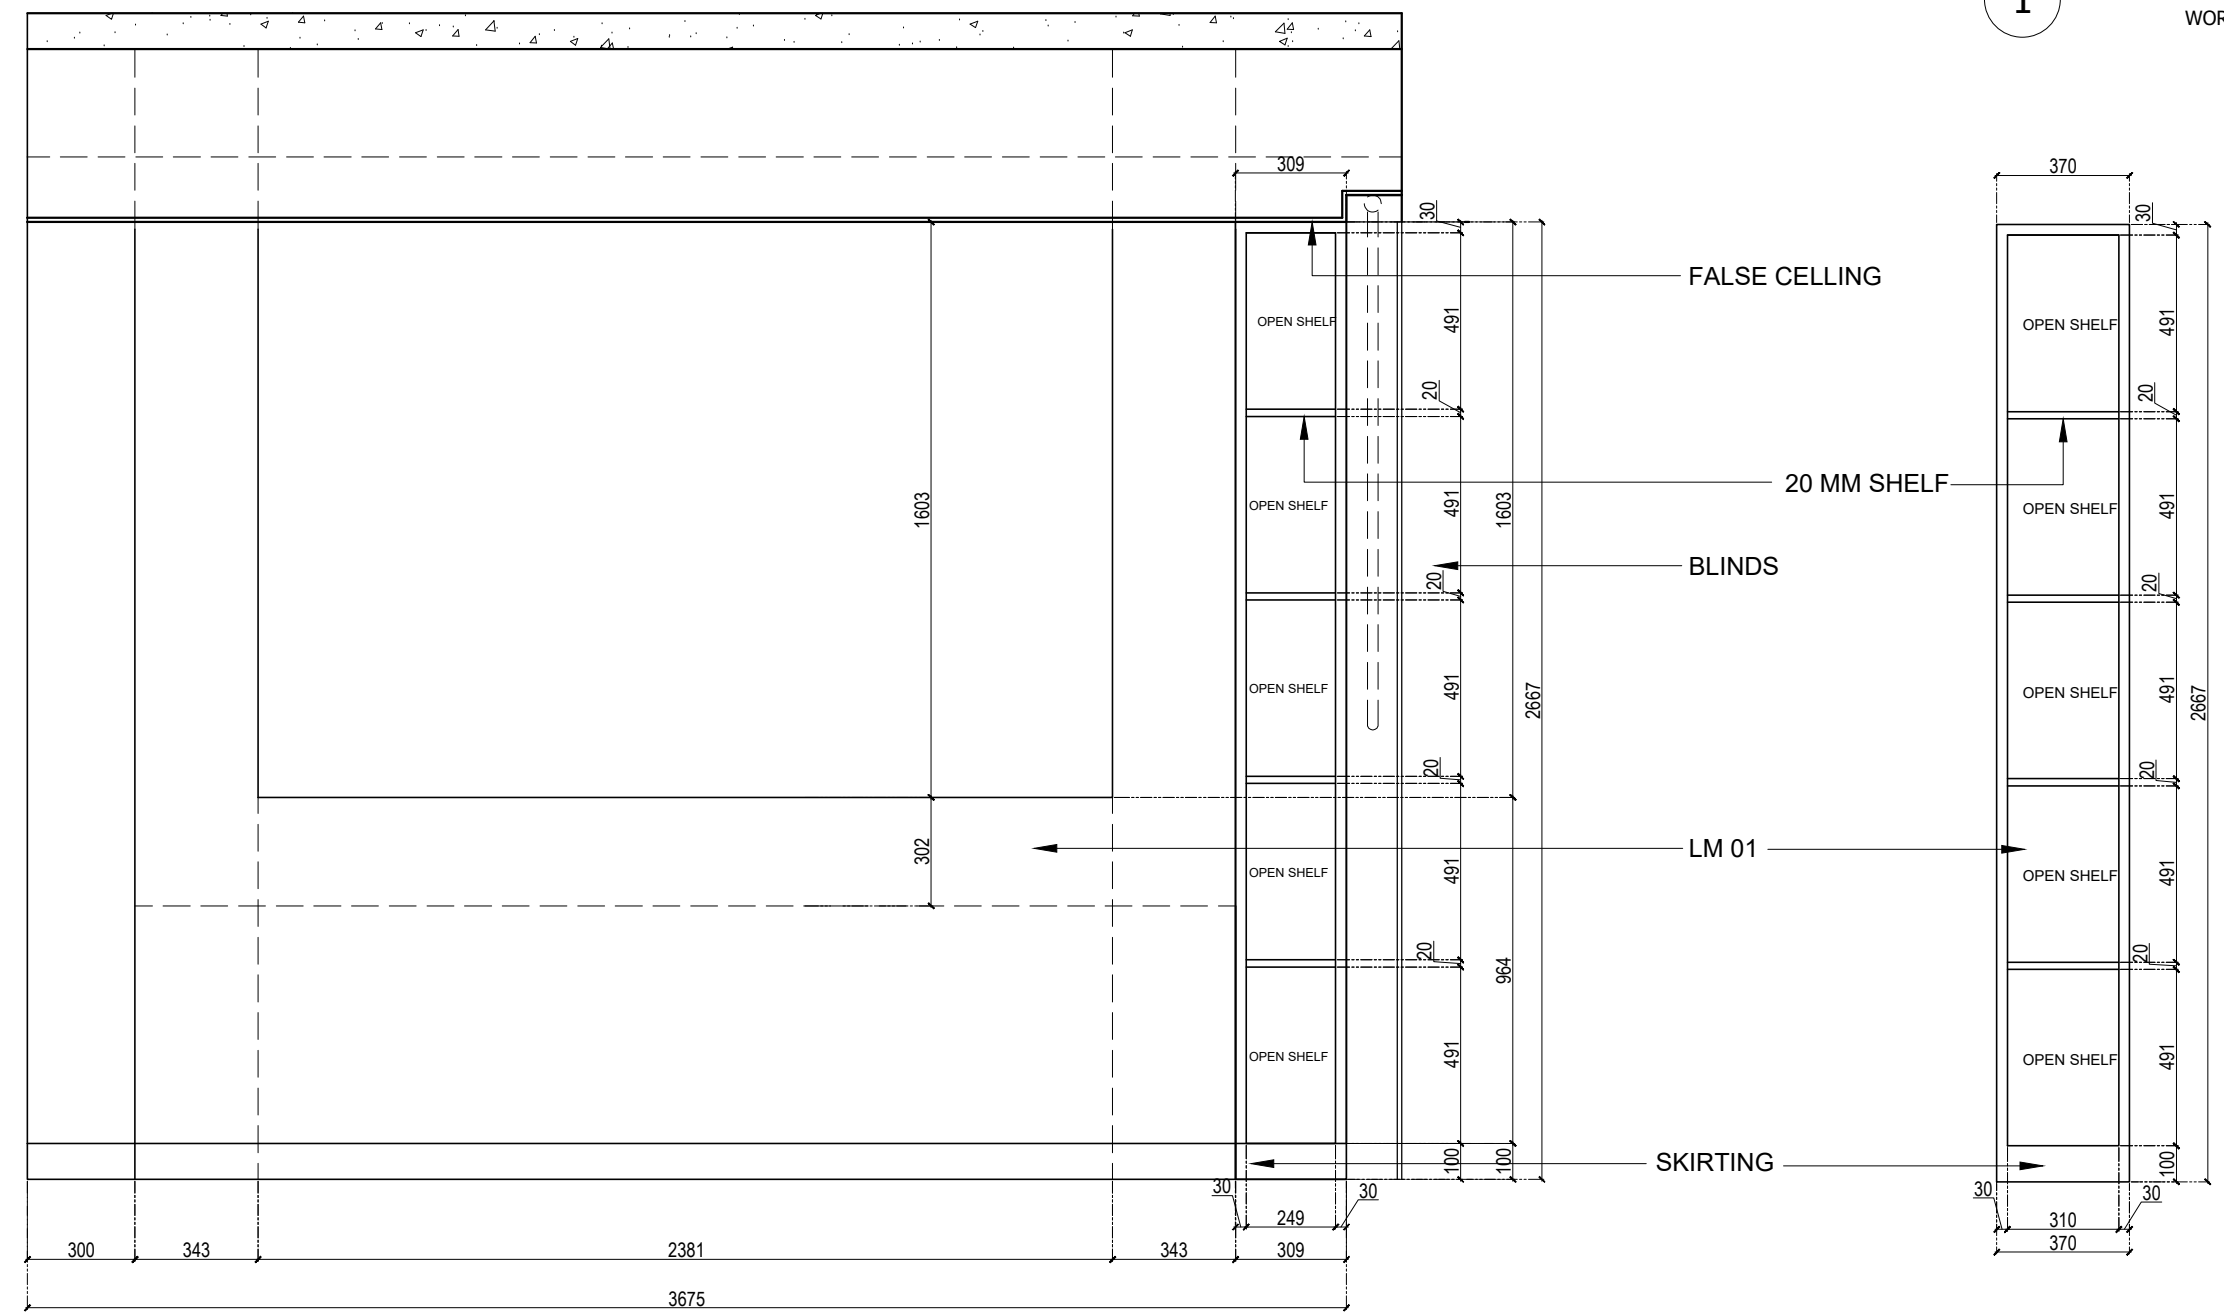

2.1 FRONT ELEVATION
WORKSTATION AREA PLANTER BOX

3 ELEVATION AT A
WORKSTATION AREA PLANTER BOX

WORKSTATION AREA PLANTER BOX